GENERAL NOTES:


1 DO NOT SCALE FROM THIS DRAWING. USE FIGURED DIMENSIONS ONLY. CHECK ALL DIMENSIONS ON SITE AND REPORT ANY DISCREPANCIES TO THE ARCHITECT.

2 ALL DIMENSIONS SHOWN IN MILLIMETERS [mm] UNLESS OTHERWISE SPECIFIED.


4 ALL WORK TO BE CARRIED OUT IN ACCORDANCE WITH APPROVED UK BUILDING REGULATIONS.

5 ALL WORK TO BE CARRIED OUT IN ACCORDANCE WITH APPROVED PLANNING DOCUMENTATION AND PARTY WALL AGREEMENTS.


6 ALL DIMENSIONS AND LEVELS ARE INDICATIVE ONLY AND ARE TBC PRIOR TO CONSTRUCTION.

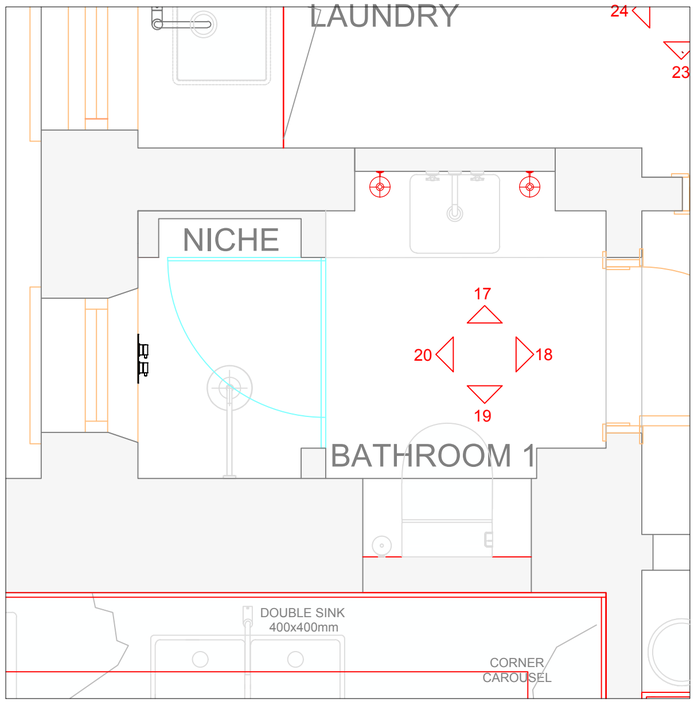

GUEST SHOWER ROOM - PLAN VIEW
Scale 1:30

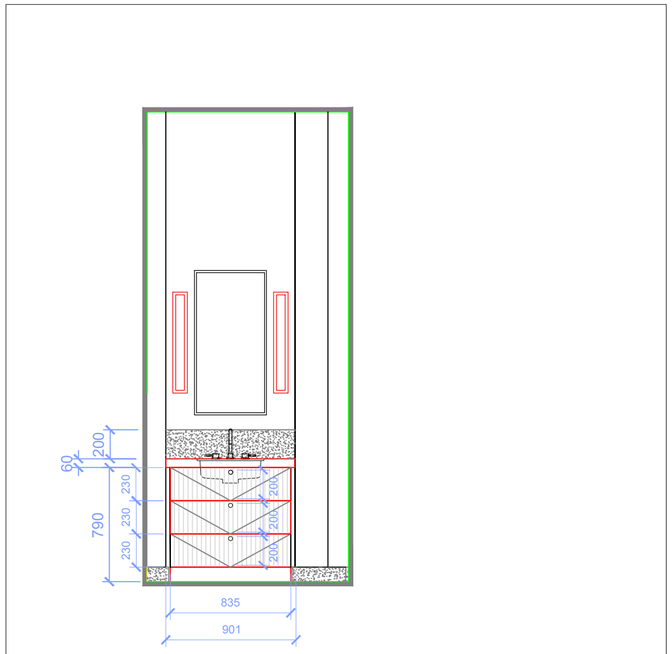

17 GUEST SHOWER ROOM VANITY - ELEVATION 17
Scale 1:30

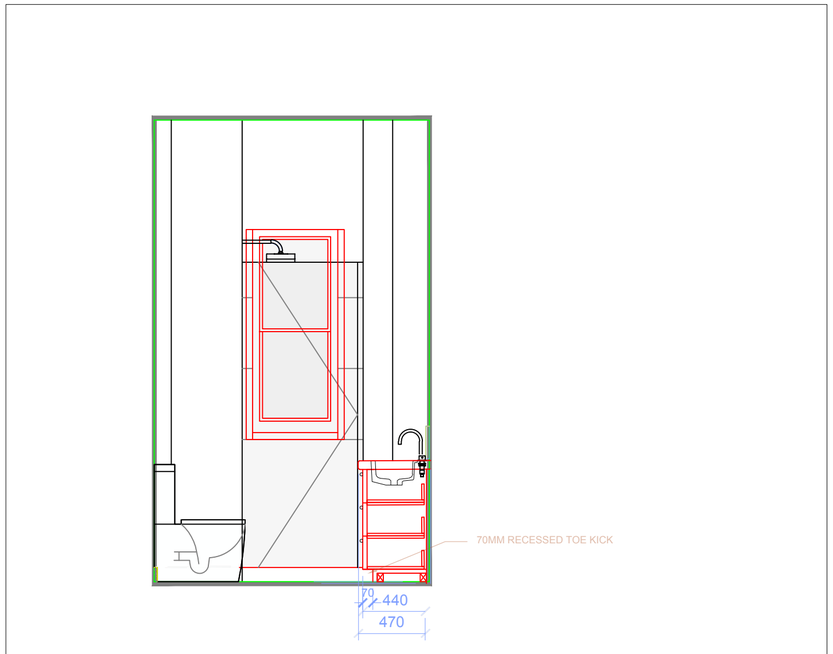

20 GUEST SHOWER ROOM VANITY - SECTION 20
Scale 1:30

HANNAH LEWINGTON
3 INKERMAN ROAD
LONDON
NW5 3BS
hannah.lewington@gmail.com
@hannahlewington

DRAWING STATUS: DRAFT JOINERY

UNLESS OTHERWISE STATED, THIS DRAWING IS FOR INFORMATION ONLY.

DO NOT SCALE THIS DRAWING!
USE FIGURED DIMENSIONS ONLY.

REV.	DATE	DESCRIPTION	REV.	DATE	DESCRIPTION	REV.	DATE	DESCRIPTION

DRAWING: **GUEST BATHROOM VANITY**

PROJECT: **36 HOLLAND PARK**

DATE: 19.05.2026

REVISION: 03


SCALE: 1:30 @ A2

PROJECT: 36HP


DRAWING NUMBER: **JOINERY_08**

GENERAL NOTES:


1. DO NOT SCALE FROM THIS DRAWING. USE FIGURED DIMENSIONS ONLY. CHECK ALL DIMENSIONS ON SITE AND REPORT ANY DISCREPANCIES TO THE ARCHITECT.
2. ALL DIMENSIONS SHOWN IN MILLIMETERS [mm] UNLESS OTHERWISE SPECIFIED.
4. ALL WORK TO BE CARRIED OUT IN ACCORDANCE WITH APPROVED UK BUILDING REGULATIONS.
5. ALL WORK TO BE CARRIED OUT IN ACCORDANCE WITH APPROVED PLANNING DOCUMENTATION AND PARTY WALL AGREEMENTS.
6. ALL DIMENSIONS AND LEVELS ARE INDICATIVE ONLY AND ARE TBC PRIOR TO CONSTRUCTION.

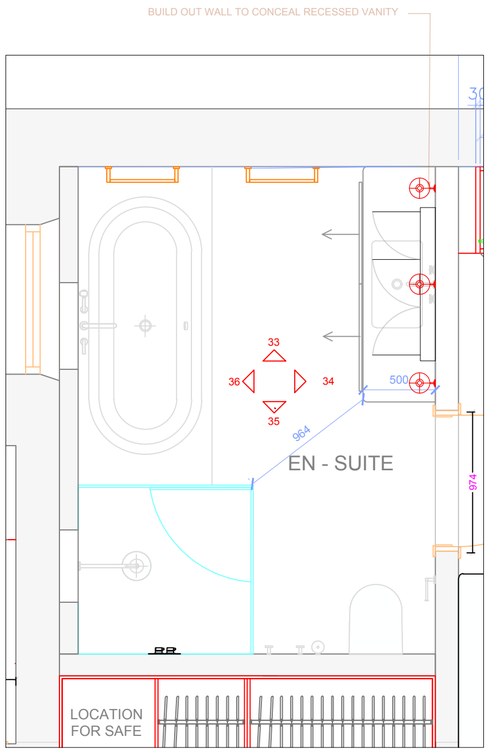

MASTER EN-SUITE - PLAN VIEW
Scale 1:30

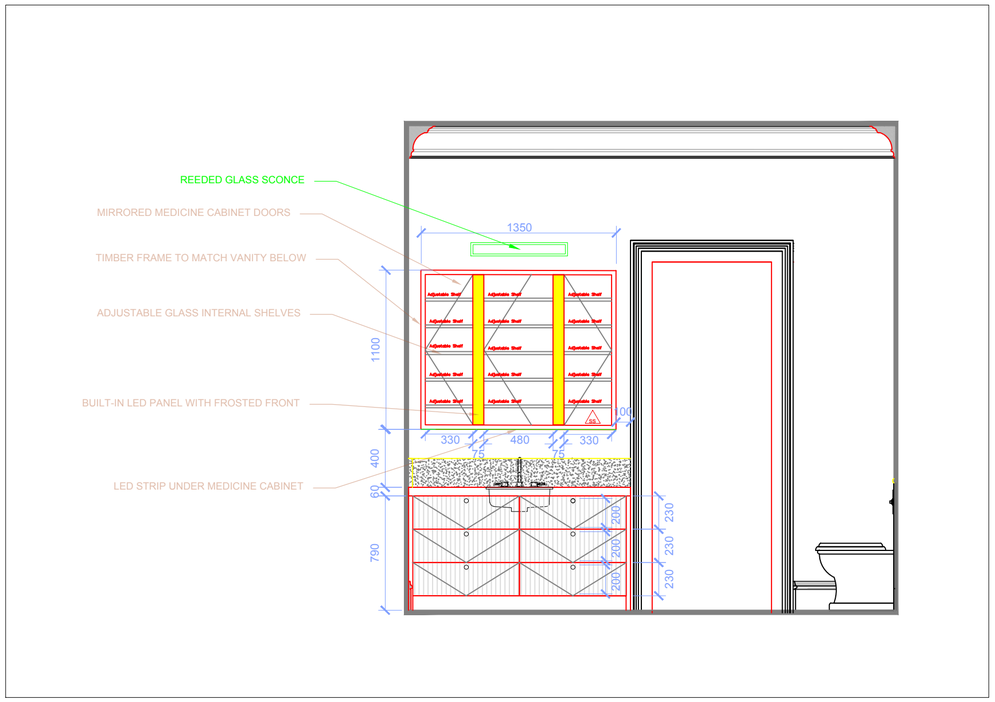

34 MASTER EN-SUITE VANITY - ELEVATION 34
Scale 1:30

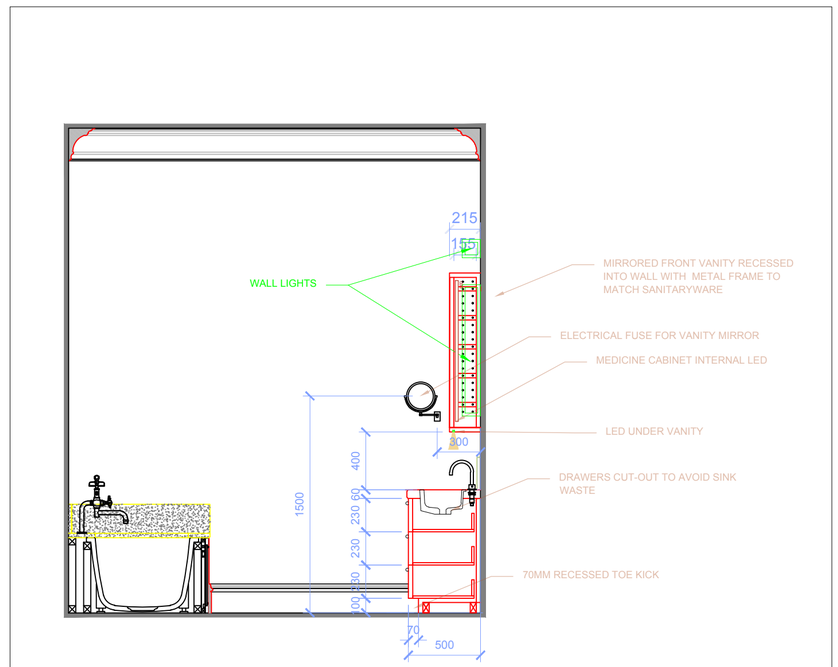

33 MASTER EN-SUITE VANITY - SECTION 33
Scale 1:30

HANNAH LEWINGTON
3 INKERMAN ROAD
LONDON
NW5 3BS
hannah.lewington@gmail.com
@hannahlewington

DRAWING STATUS: DRAFT JOINERY

UNLESS OTHERWISE STATED, THIS DRAWING IS FOR INFORMATION ONLY.

DO NOT SCALE THIS DRAWING! USE FIGURED DIMENSIONS ONLY.

REV.	DATE	DESCRIPTION	REV.	DATE	DESCRIPTION	REV.	DATE	DESCRIPTION

DRAWING: **MASTER BATHROOM VANITY**

PROJECT: **36 HOLLAND PARK**

DATE: 22.05.2026

REVISION: 04

SCALE: 1:30 @ A2

PROJECT: 36HP

DRAWING NUMBER: **JOINERY_09**