

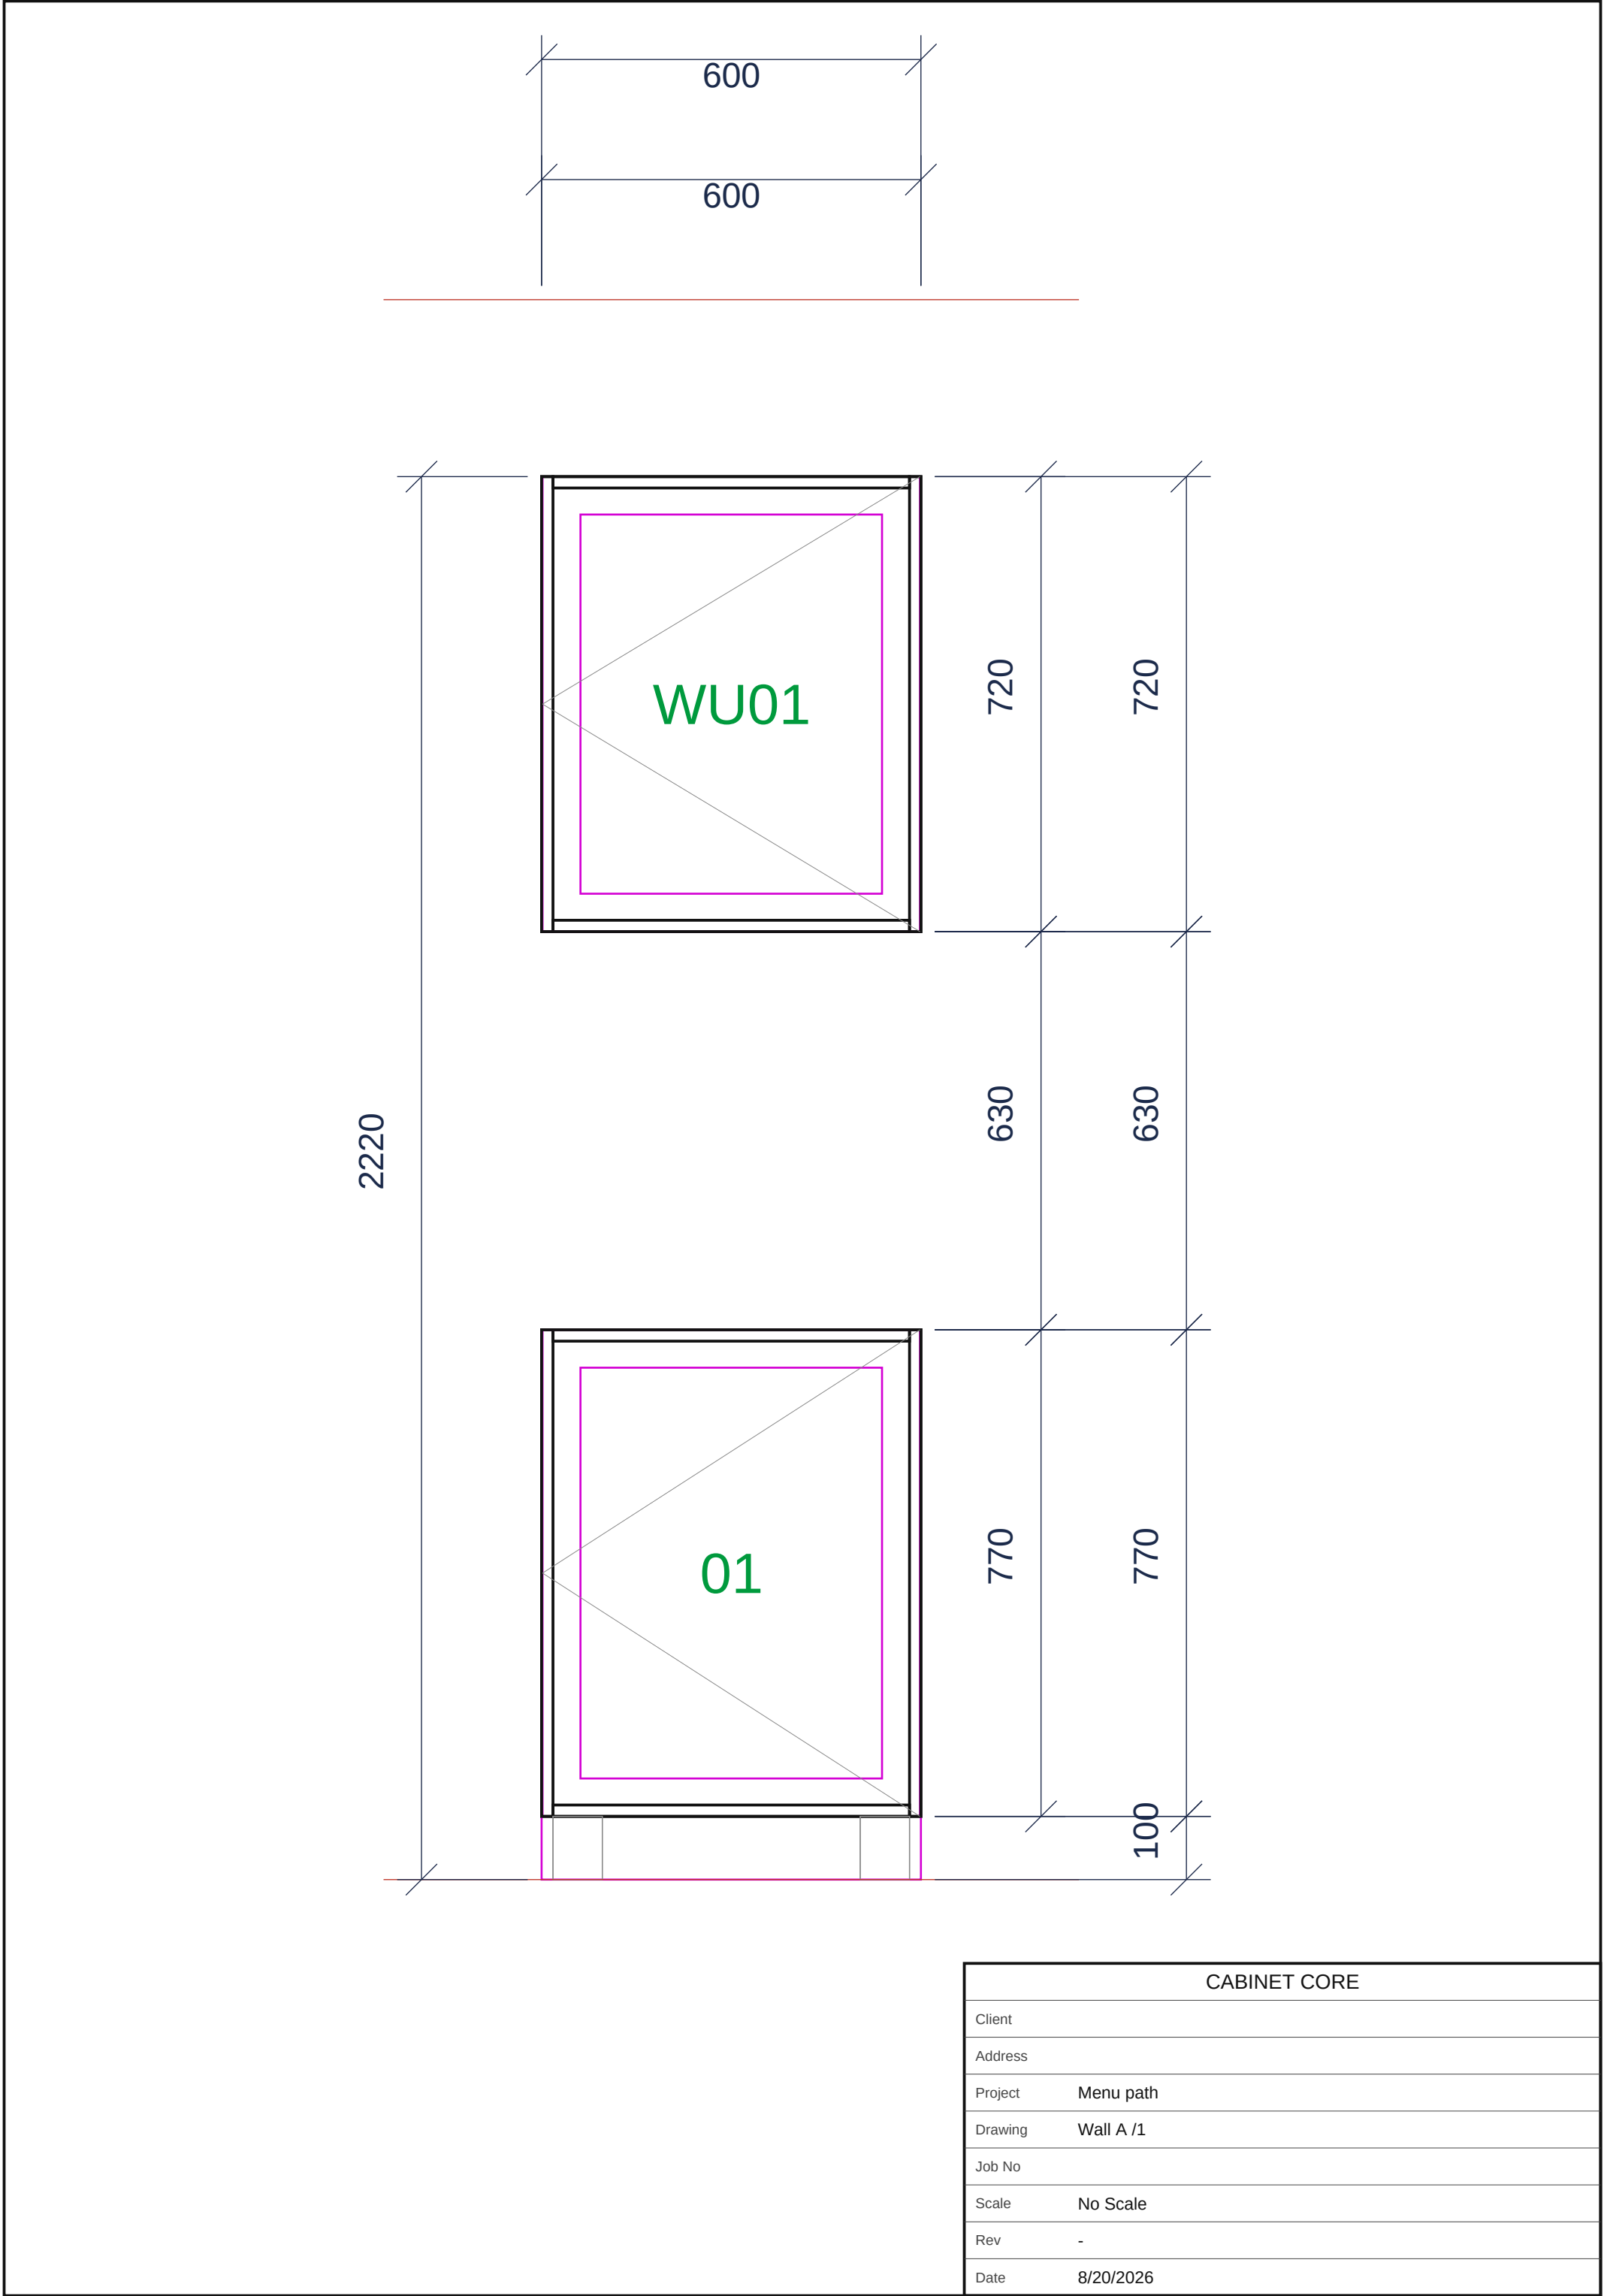


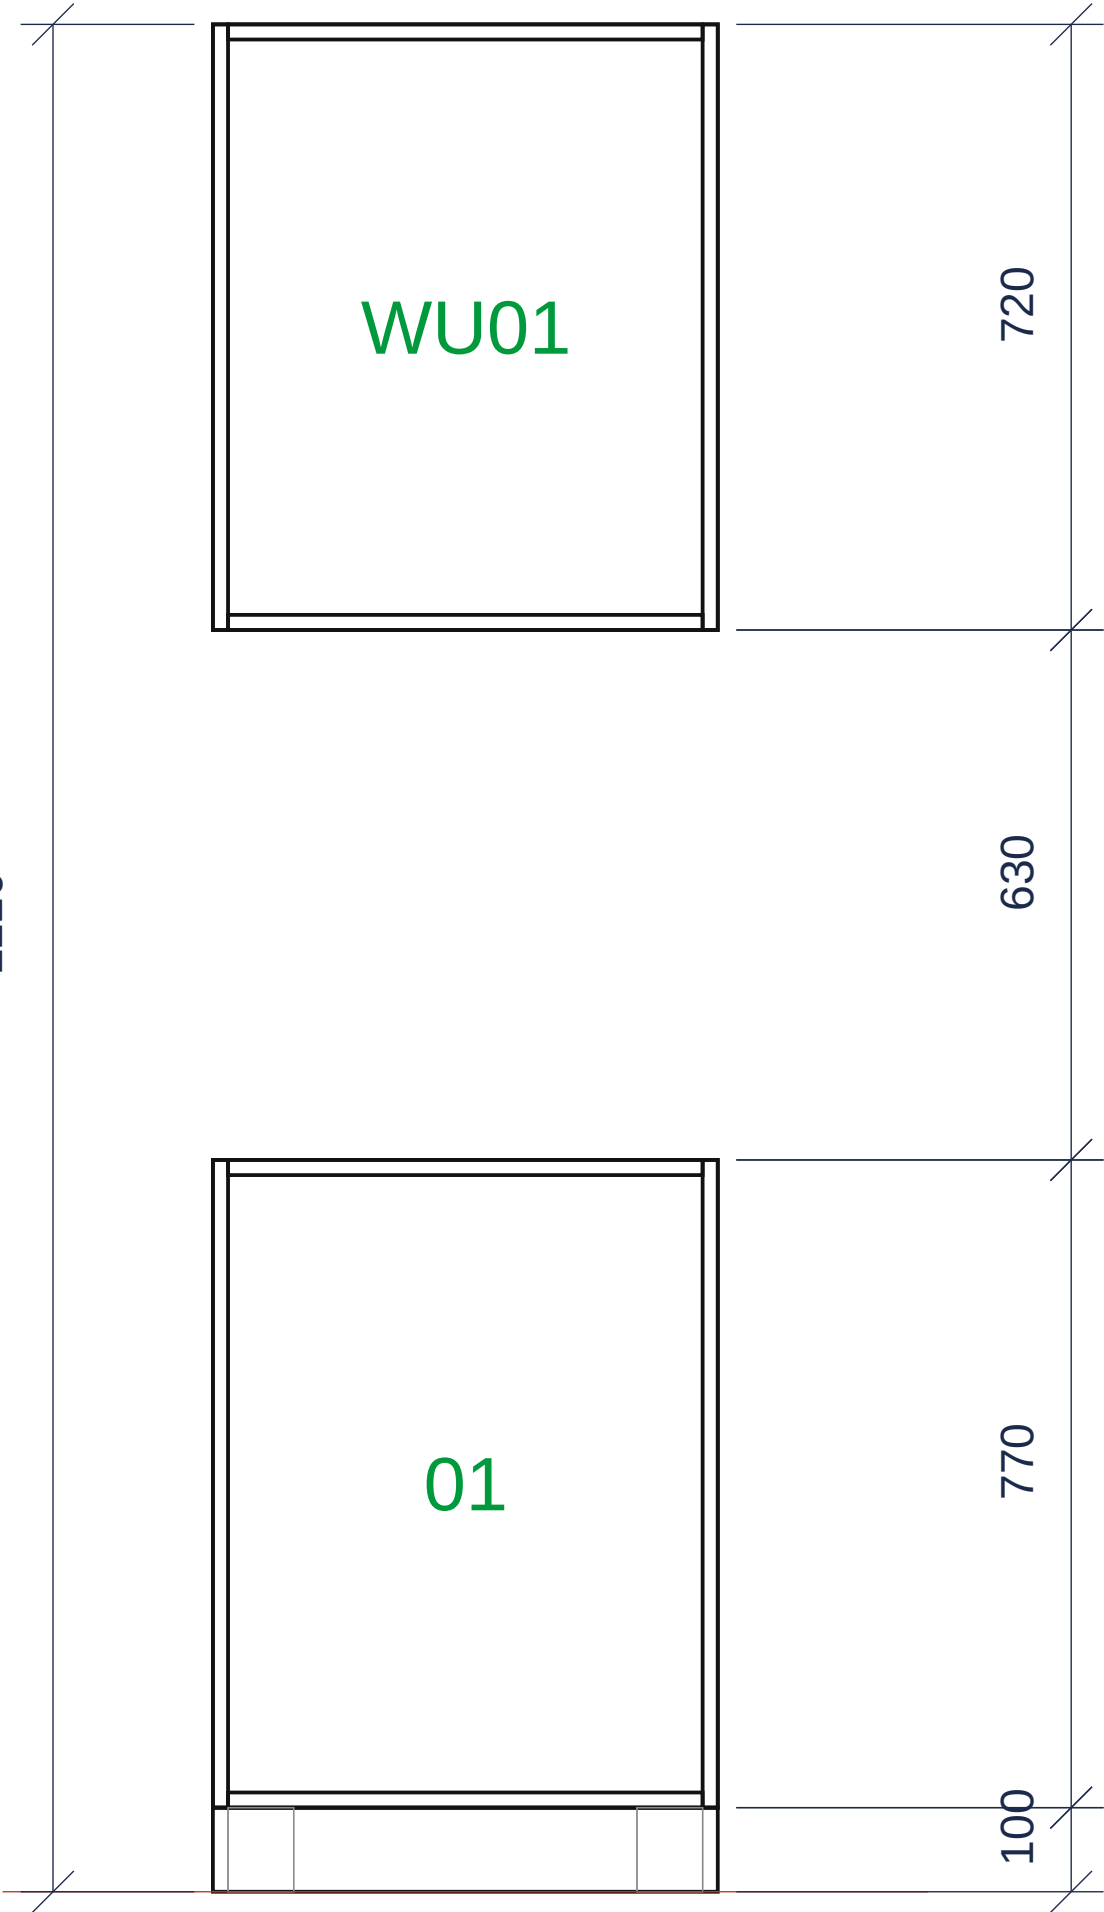

CABINET CORE	
Client	
Address	
Project	Menu path
Drawing	Wall A /1
Job No	
Scale	No Scale
Rev	-
Date	8/20/2026

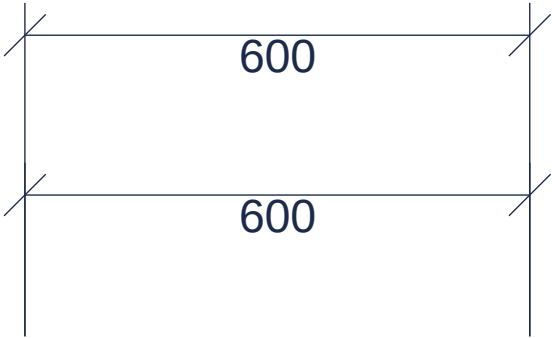

CABINET CORE	
Client	
Address	
Project	Menu path
Drawing	Wall A /2
Job No	
Scale	No Scale
Rev	-
Date	8/20/2026

WALL D

WALL B

WALL C



WALL A

CABINET CORE	
Client	
Address	
Project	Menu path
Drawing	Horizontal section
Job No	
Scale	No Scale
Rev	-
Date	8/20/2026