


FITTED FURNITURE

3-7 Herbal Hill, 1st floor

Client AP&W · Job 032/2026 · Rev A · Issued 08.02.2026 · Status B, For approval

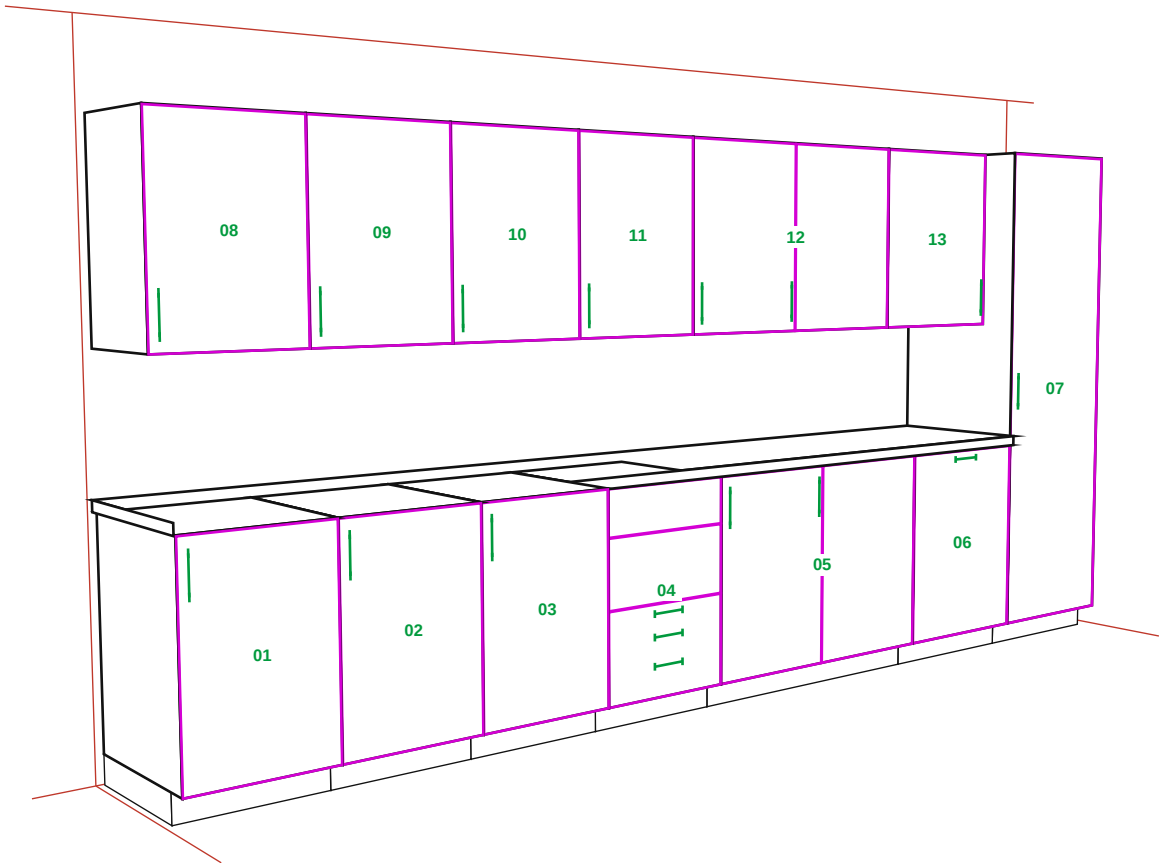

Perspective as on its own sheet. The visualisation sheet carries the render.

DRAWING CONVENTIONS

- Fronts (doors, drawer fronts)
- Carcass
- Hidden / above the cut
- Unit number
- Hardware, appliance space
- Building (walls, floor, ceiling)
- Dimensions in mm

GENERAL NOTES

- All dimensions in millimetres. Do not scale off this drawing; work to figured dimensions.
- Carcass and fronts as the cut list, sheet with the materials.
- Appliances and worktop are shown for position only, supplied by others unless stated.
- Site dimensions to be checked before cutting.

SHEET INDEX

No	Drawing	Scale	Rev
00	Cover, index and revisions	n/a	A
01	Plan · base units	1:20 @ A3	A
02	Plan · wall units	1:20 @ A3	A
03	Wall A · Front view	1:20 @ A3	A
04	Wall A · Internal layout	1:20 @ A3	A
05	Wall A · Sections A-A and B-B	1:15 @ A3	A
06	Wall A · Perspective view	NTS	A
07	Visualisation	NTS	A
08	Cut list and materials	n/a	A

REVISIONS

Rev	Date	Description	By
A	08.02.2026	First issue	PT

STATUS

- ☐ A Preliminary
- ☒ B For approval
- ☐ C For production

Approved: _____ Date: _____

LOGO
(Settings)

CABINET CORE
Bespoke fitted furniture
London
hello@cabinetcore.example

CLIENT

AP&W

SITE ADDRESS

3-7 Herbal Hill, 1st floor

PROPERTY OF

CABINET CORE. Not to be copied without consent.

PROJECT

3-7 Herbal Hill, 1st floor

DRAWING

00 · Cover, index and revisions

DRAWING No

032-2026-00

DRAWN

PT

CHECKED

DATE

08.02.2026

JOB No

032/2026

SCALE

n/a

PAPER

A3

REV


A

SHEET


00 / 09

01 • PLAN • BASE UNITS

Horizontal section at 400 above FFL, looking down. Wall units not shown.

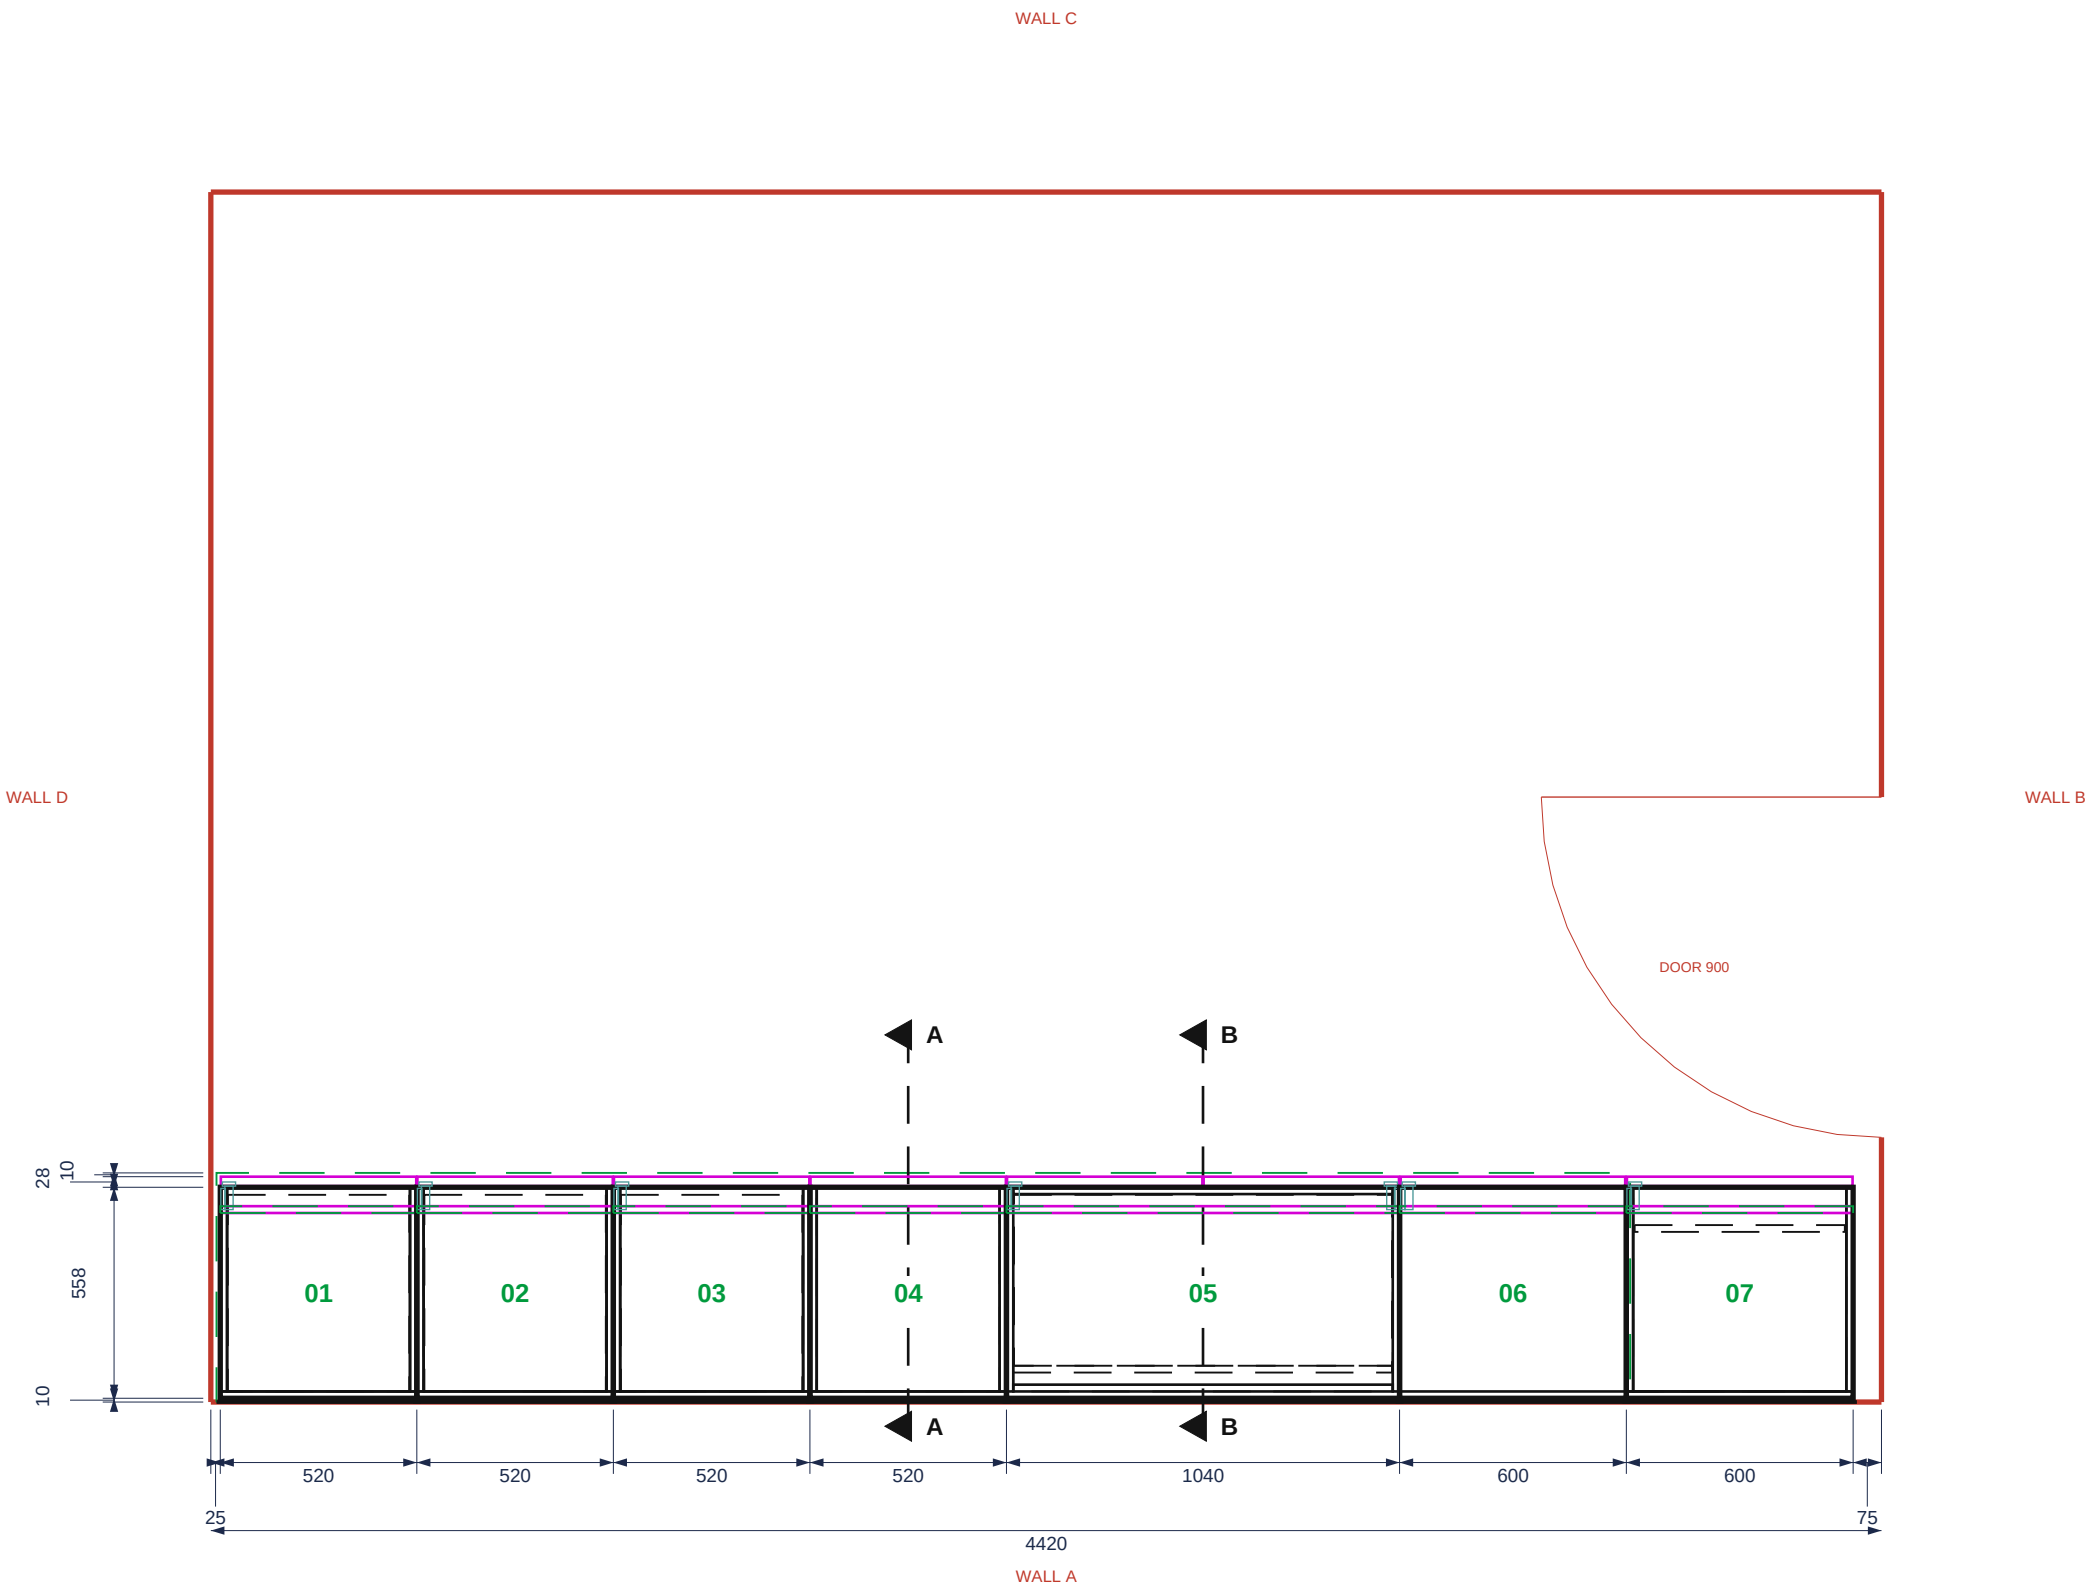

KEY PLAN

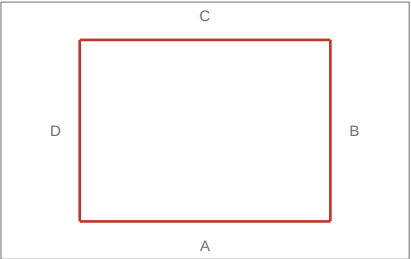

LEGEND

- Fronts (doors, drawer fronts)
- Carcass
- Hidden / above the cut
- Unit number
- Hardware, appliance space
- Building (walls, floor, ceiling)
- Dimensions in mm

NOTES

- All dimensions in millimetres. Do not scale off this drawing; work to figured dimensions.
- Carcass and fronts as the cut list, sheet with the materials.
- Appliances and worktop are shown for position only, supplied by others unless stated.
- Site dimensions to be checked before cutting.

STATUS

- A Preliminary
- B For approval
- C For production

Approved:

Date:

LOGO
(Settings)

CABINET CORE

Bespoke fitted furniture

London

hello@cabinetcore.example

CLIENT

AP&W

SITE ADDRESS

3-7 Herbal Hill, 1st floor

PROPERTY OF

CABINET CORE. Not to be copied without consent.

PROJECT

3-7 Herbal Hill, 1st floor

DRAWING

01 • Plan • base units

DRAWING No

032-2026-01

DRAWN

PT

CHECKED

DATE

08.02.2026

JOB No

032/2026

SCALE

1:20 @ A3

PAPER

A3

REV


A

SHEET


01 / 09

02 · PLAN · WALL UNITS

Horizontal section at 1700 above FFL, looking down. The worktop is seen below the cut.

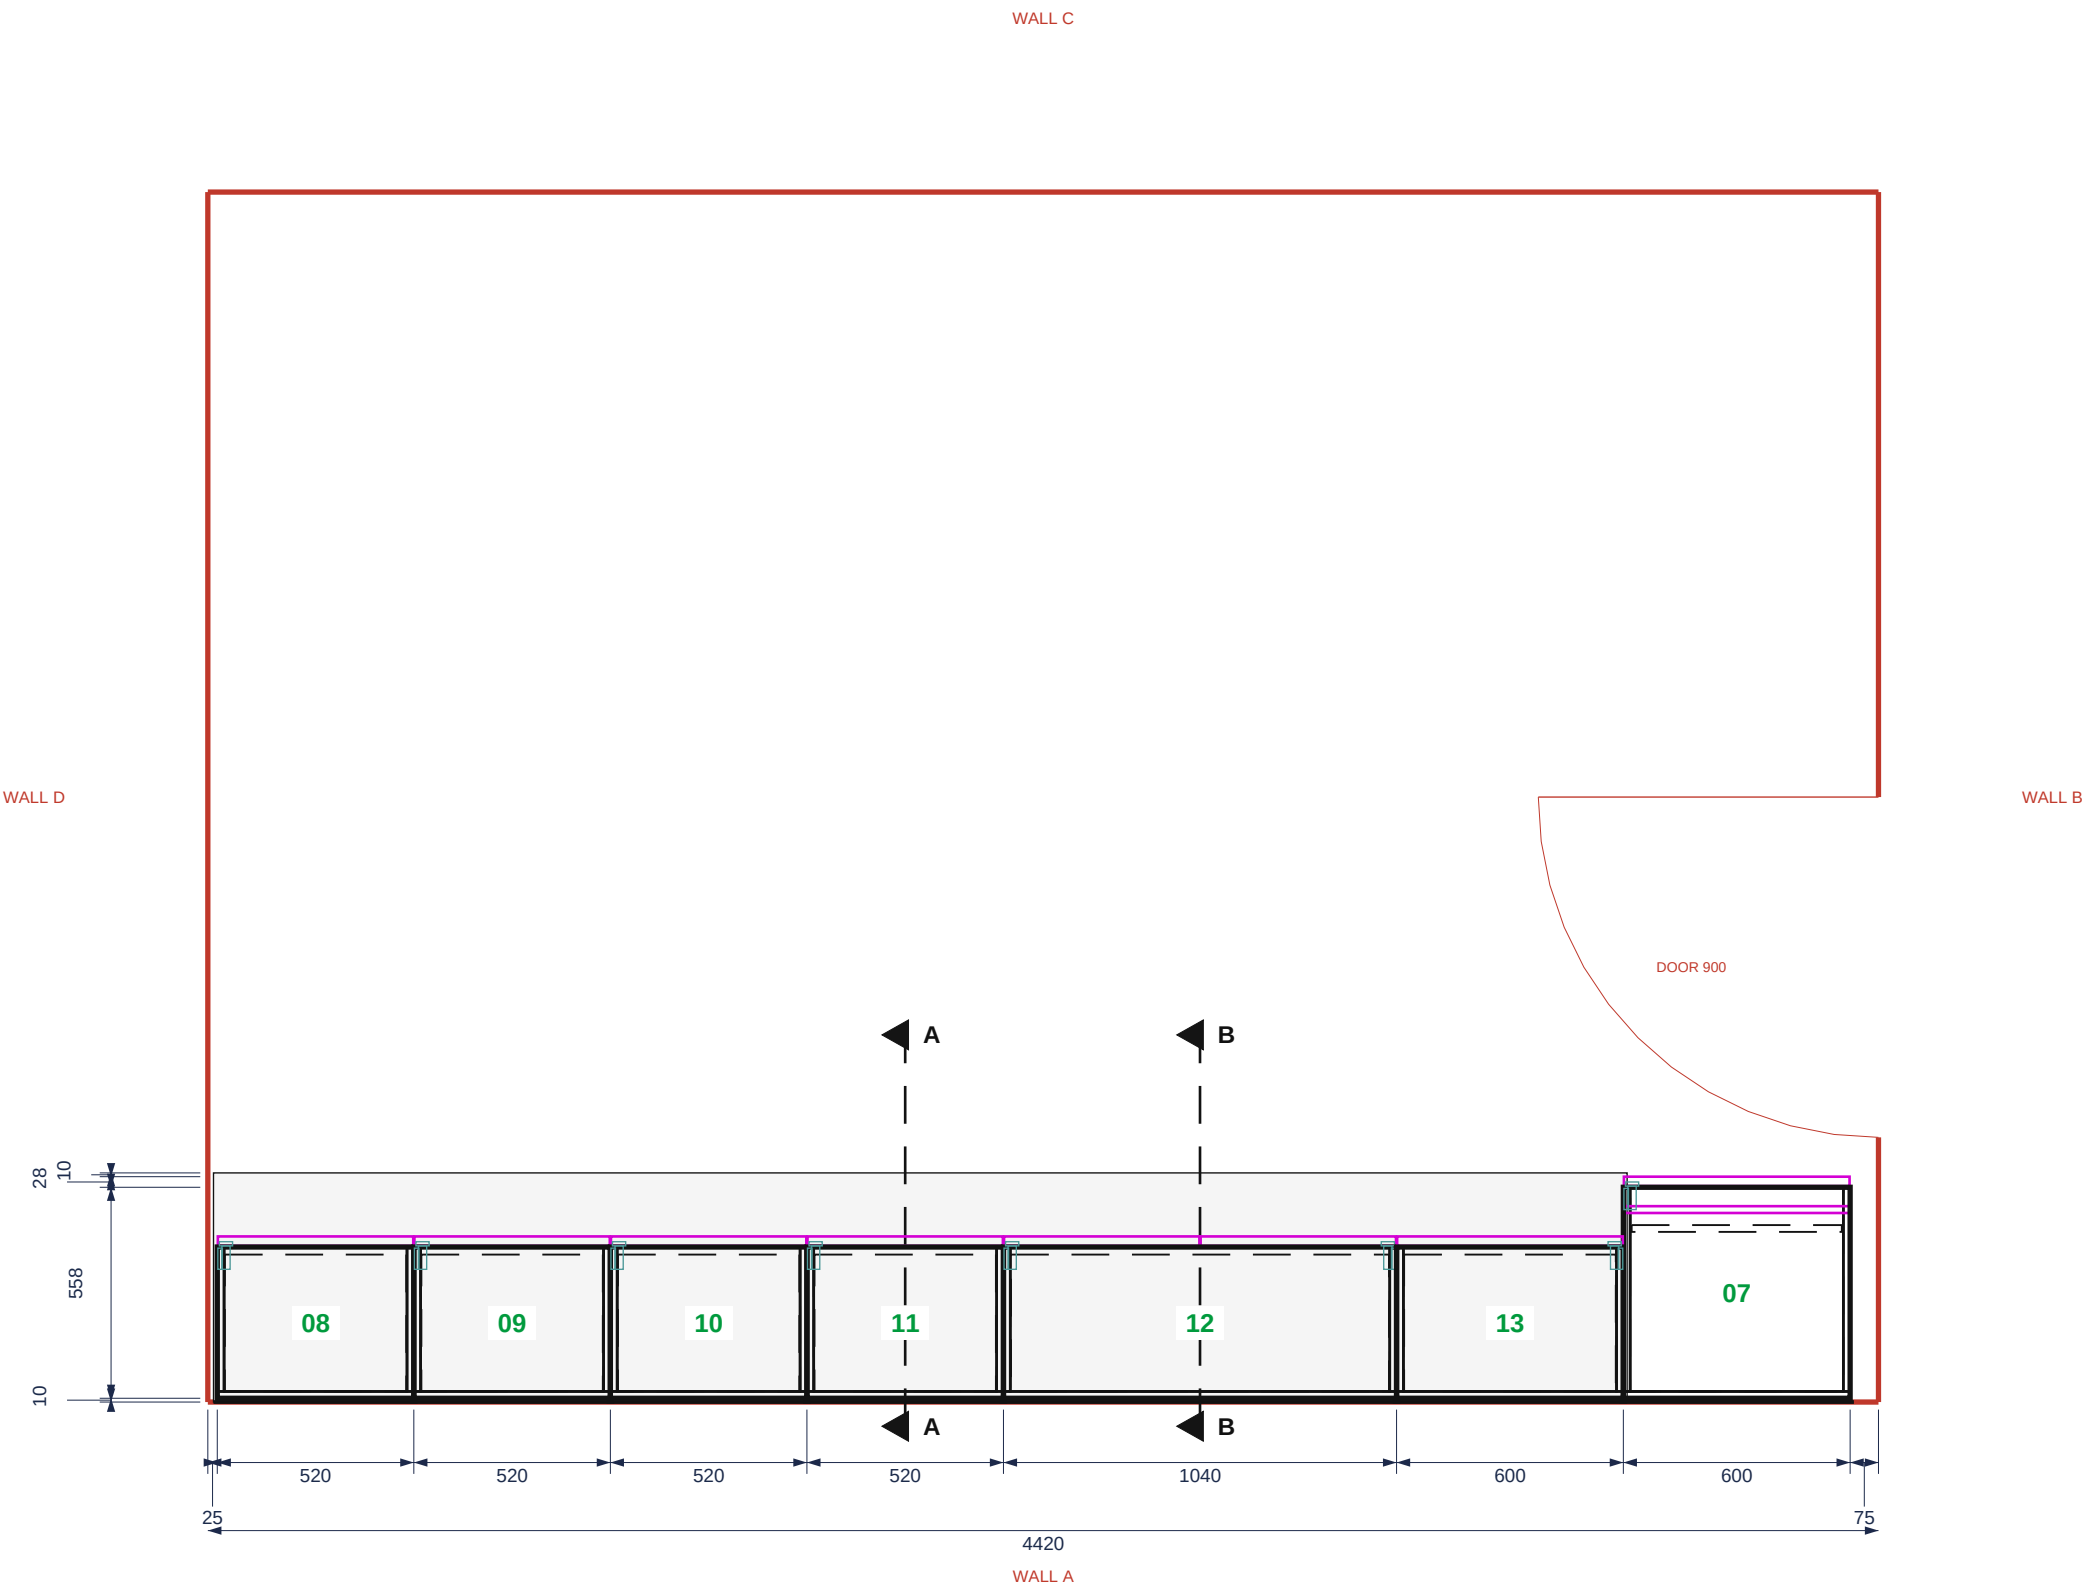

KEY PLAN

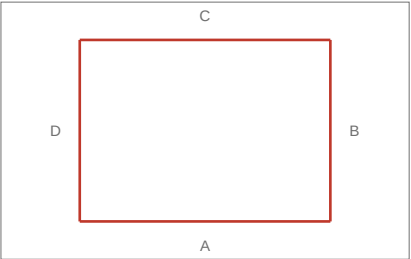

LEGEND

- Fronts (doors, drawer fronts)
- Carcass
- Hidden / above the cut
- Unit number
- Hardware, appliance space
- Building (walls, floor, ceiling)
- Dimensions in mm

NOTES

- All dimensions in millimetres. Do not scale off this drawing; work to figured dimensions.
- Carcass and fronts as the cut list, sheet with the materials.
- Appliances and worktop are shown for position only, supplied by others unless stated.
- Site dimensions to be checked before cutting.

STATUS

- A Preliminary
- B For approval
- C For production

Approved: Date:

LOGO
(Settings)

CABINET CORE

Bespoke fitted furniture
London
hello@cabinetcore.example

CLIENT

AP&W

SITE ADDRESS

3-7 Herbal Hill, 1st floor

PROPERTY OF

CABINET CORE. Not to be copied without consent.

PROJECT

3-7 Herbal Hill, 1st floor

DRAWING

02 · Plan · wall units

DRAWING No

032-2026-02

DRAWN

PT

CHECKED

DATE

08.02.2026

JOB No

032/2026

SCALE

1:20 @ A3

PAPER

A3

REV


A

SHEET


02 / 09

03 · WALL A · FRONT VIEW

Fronts on, looking at the wall from the room. Panel sizes: see the cut list.

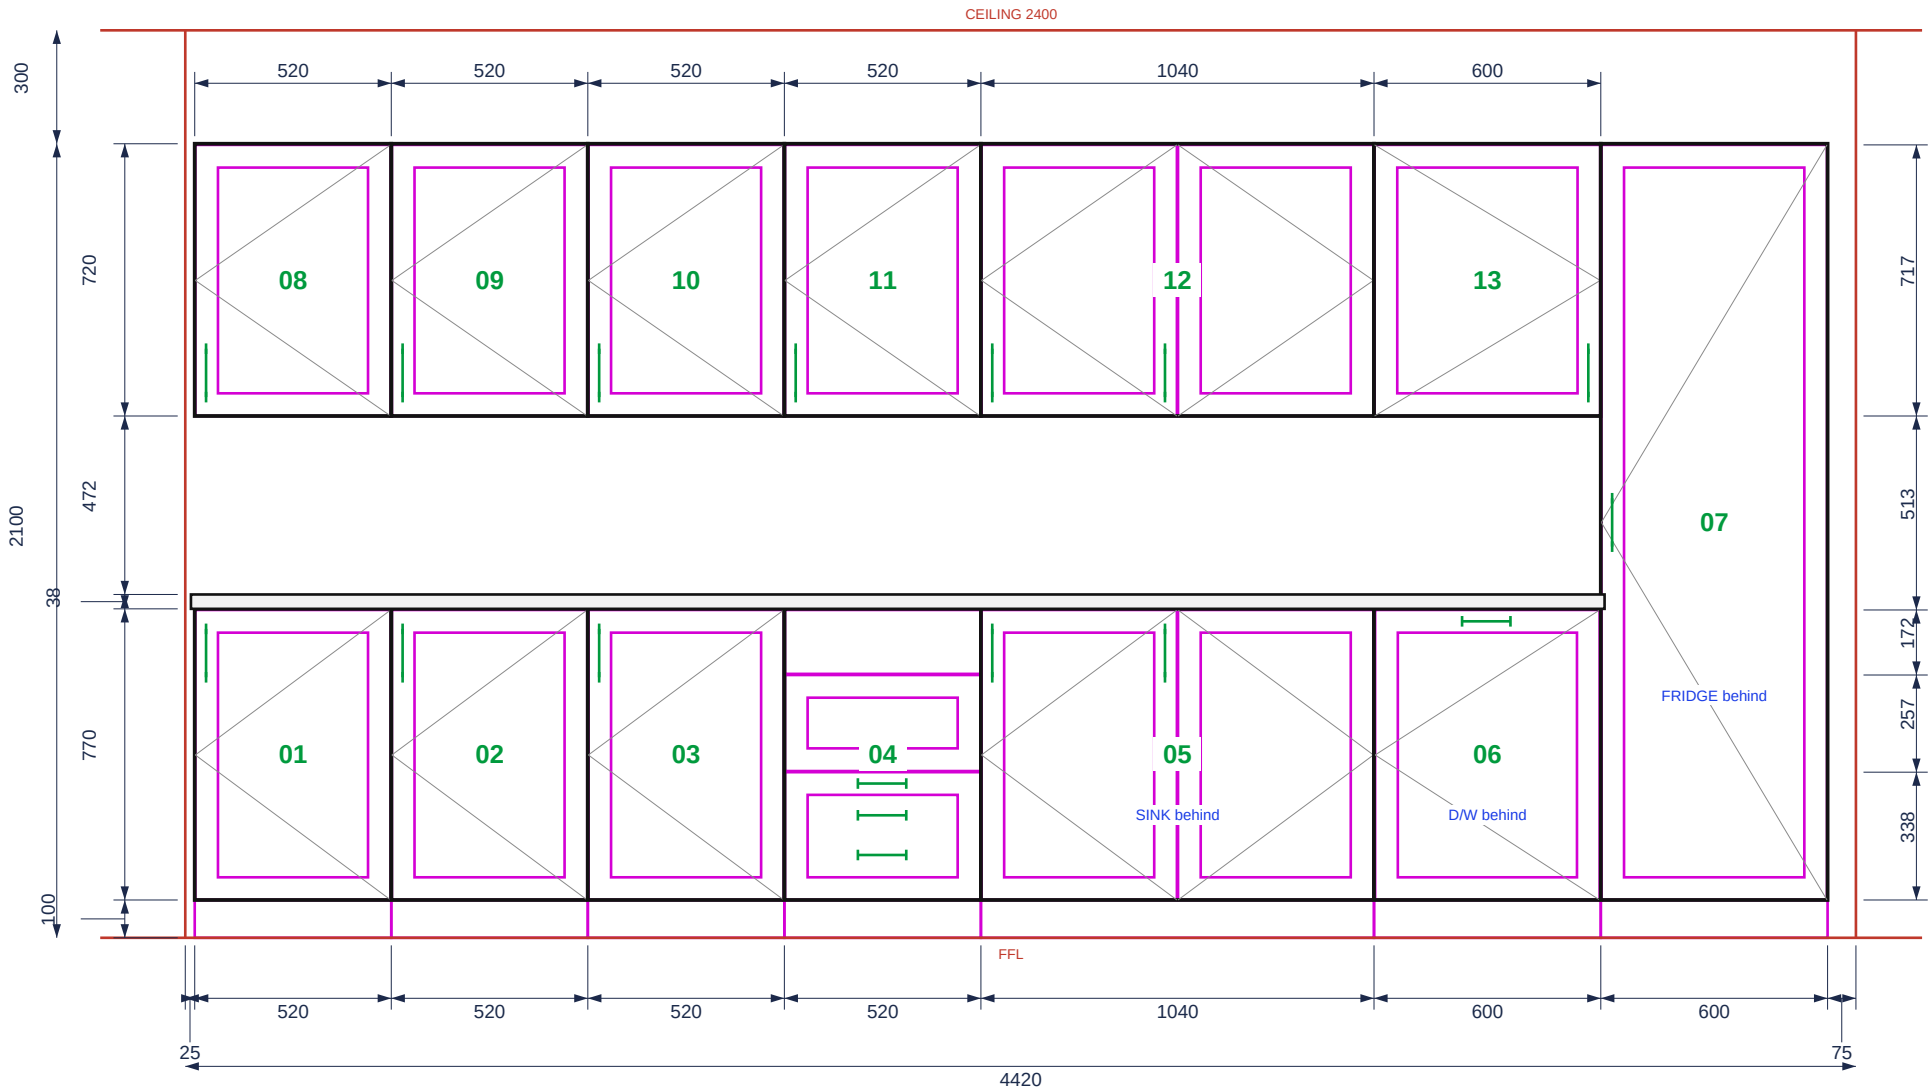

KEY PLAN

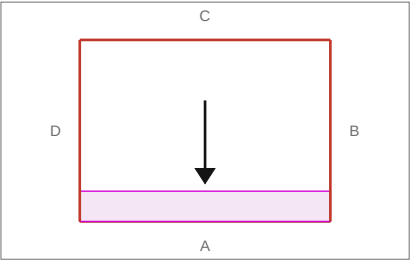

LEGEND

- Fronts (doors, drawer fronts)
- Carcass
- Hidden / above the cut
- Unit number
- Hardware, appliance space
- Building (walls, floor, ceiling)
- Dimensions in mm

NOTES

- All dimensions in millimetres. Do not scale off this drawing; work to figured dimensions.
- Carcass and fronts as the cut list, sheet with the materials.
- Appliances and worktop are shown for position only, supplied by others unless stated.
- Site dimensions to be checked before cutting.

STATUS

- A Preliminary
- B For approval
- C For production

Approved: Date:

LOGO
(Settings)

CABINET CORE

Bespoke fitted furniture
London
hello@cabinetcore.example

CLIENT

AP&W

SITE ADDRESS

3-7 Herbal Hill, 1st floor

PROPERTY OF

CABINET CORE. Not to be copied without consent.

PROJECT

3-7 Herbal Hill, 1st floor

DRAWING

03 · Wall A · Front view

DRAWING No

032-2026-03

DRAWN

PT

CHECKED

DATE

08.02.2026

JOB No

032/2026

SCALE

1:20 @ A3

PAPER

A3

REV



A

SHEET

03 / 09

04 · WALL A · INTERNAL LAYOUT

Fronts removed: carcasses, shelves, drawer boxes, hinge plates, legs and appliance spaces.

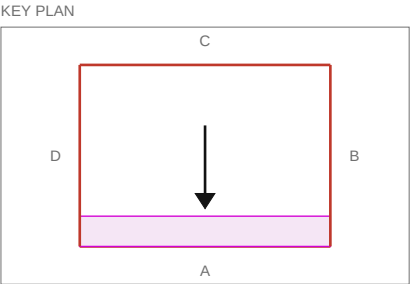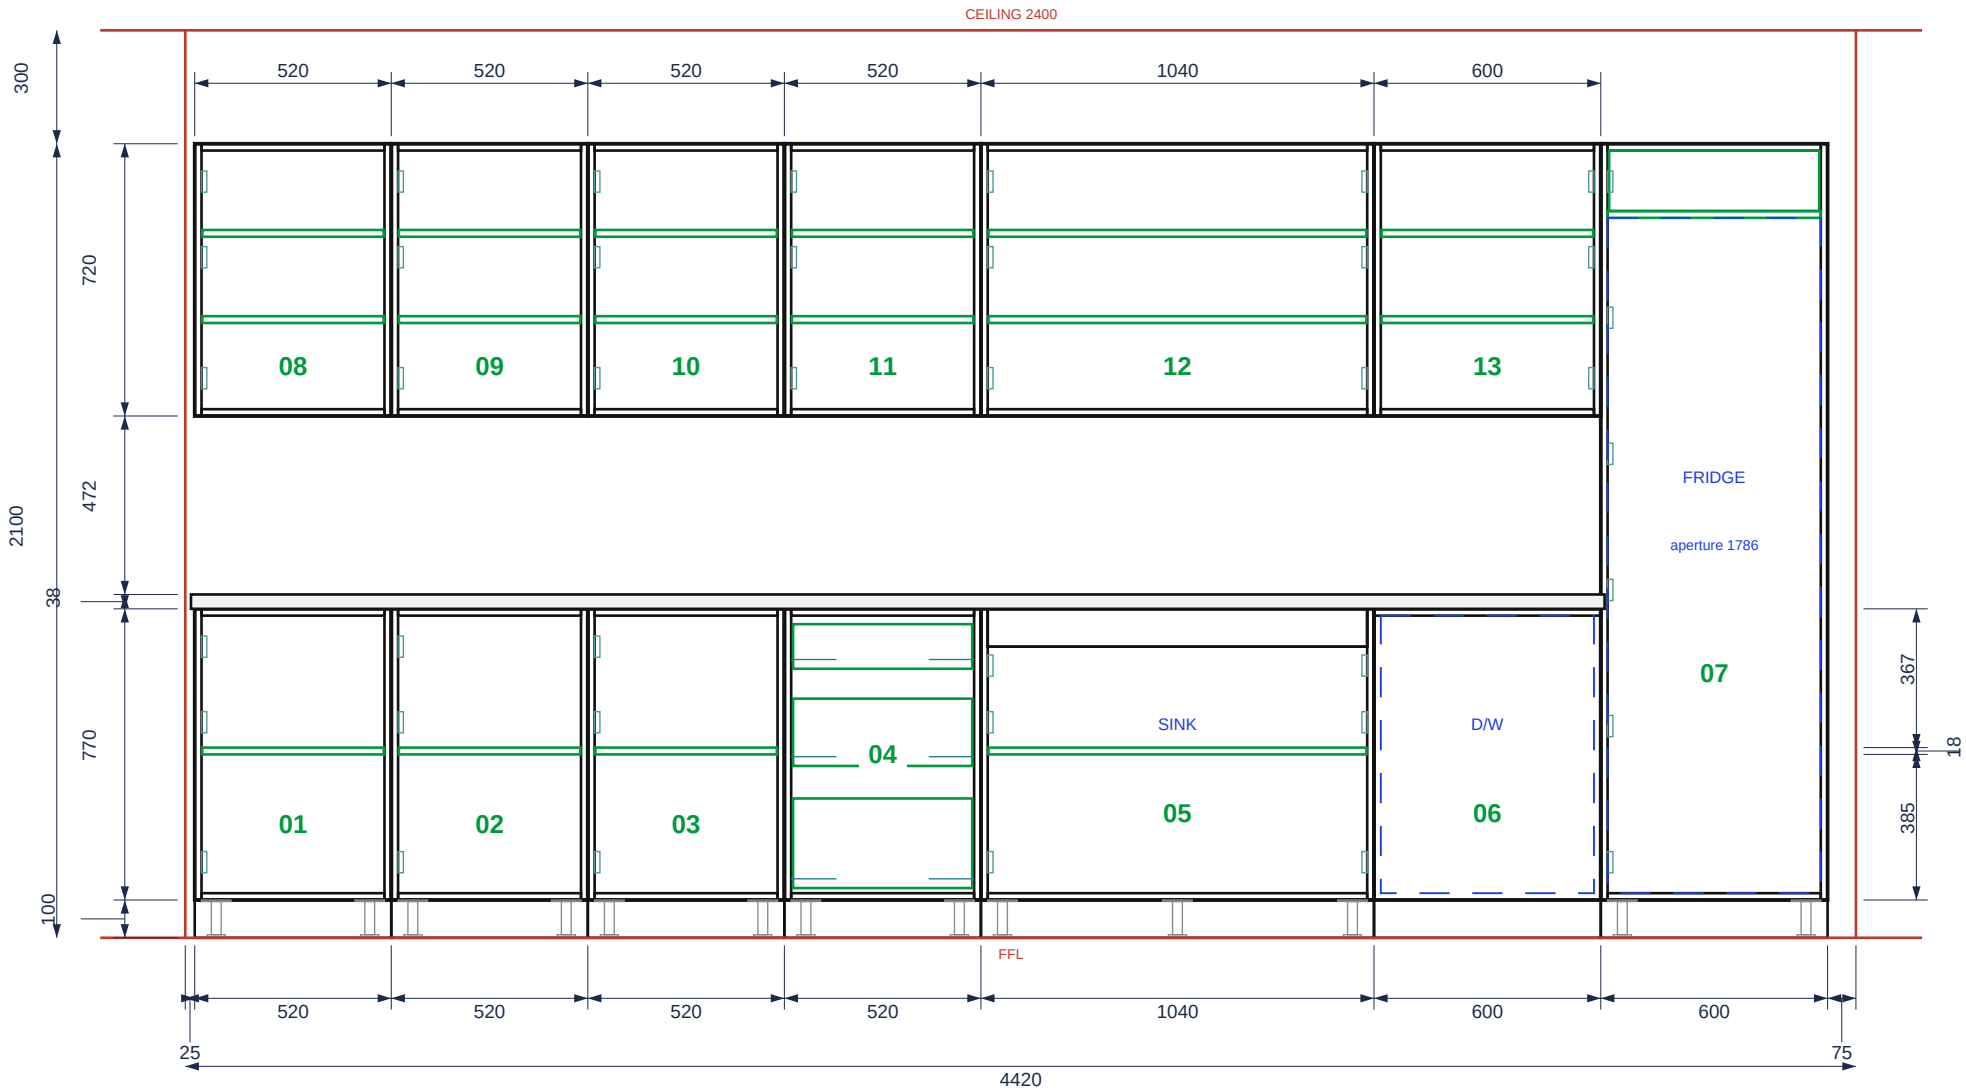

- LEGEND
- Fronts (doors, drawer fronts)
 - Carcass
 - Hidden / above the cut
 - Unit number
 - Hardware, appliance space
 - Building (walls, floor, ceiling)
 - Dimensions in mm

- NOTES
- All dimensions in millimetres. Do not scale off this drawing; work to figured dimensions.
 - Carcass and fronts as the cut list, sheet with the materials.
 - Appliances and worktop are shown for position only, supplied by others unless stated.
 - Site dimensions to be checked before cutting.

STATUS

A Preliminary

B For approval

C For production

Approved: _____ Date: _____

LOGO

(Settings)

CABINET CORE

Bespoke fitted furniture

London

hello@cabinetcore.example

CLIENT

AP&W

SITE ADDRESS

3-7 Herbal Hill, 1st floor

PROPERTY OF

CABINET CORE. Not to be copied without consent.

PROJECT

3-7 Herbal Hill, 1st floor

DRAWING

04 · Wall A · Internal layout

DRAWING No

032-2026-04

DRAWN

PT

CHECKED

DATE

08.02.2026

JOB No

032/2026

SCALE

1:20 @ A3

PAPER

A3

REV


A

SHEET


04 / 09

05 · WALL A · SECTIONS A-A AND B-B

Vertical sections marked on the plans. One cut shows plinth, base unit, worktop, wall unit, wall and ceiling together.

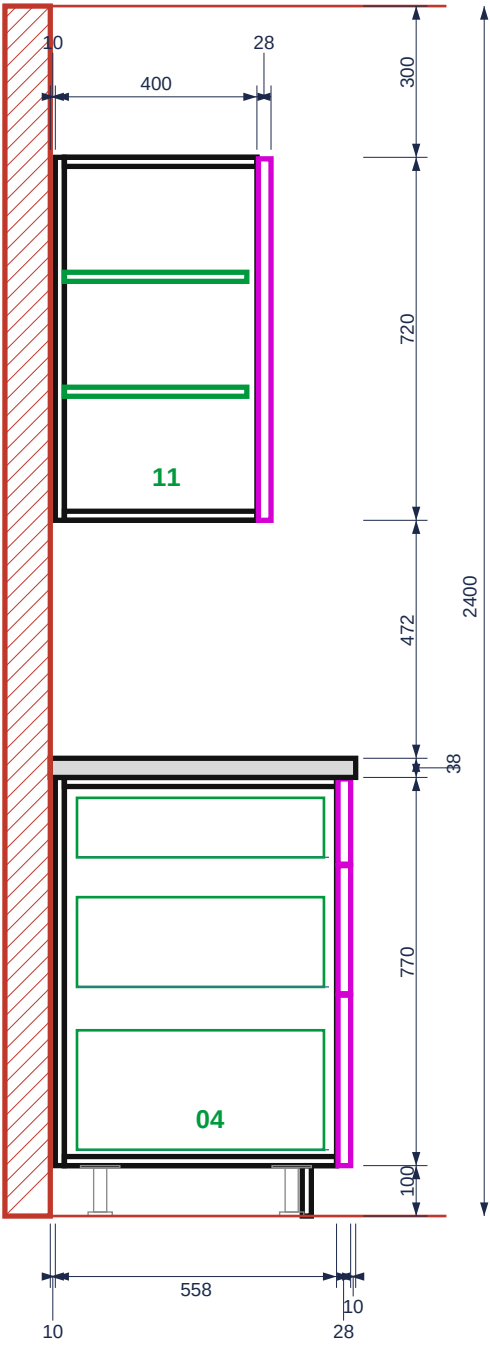


SECTION A-A · through units 04 and 11
looking along the wall, towards its start

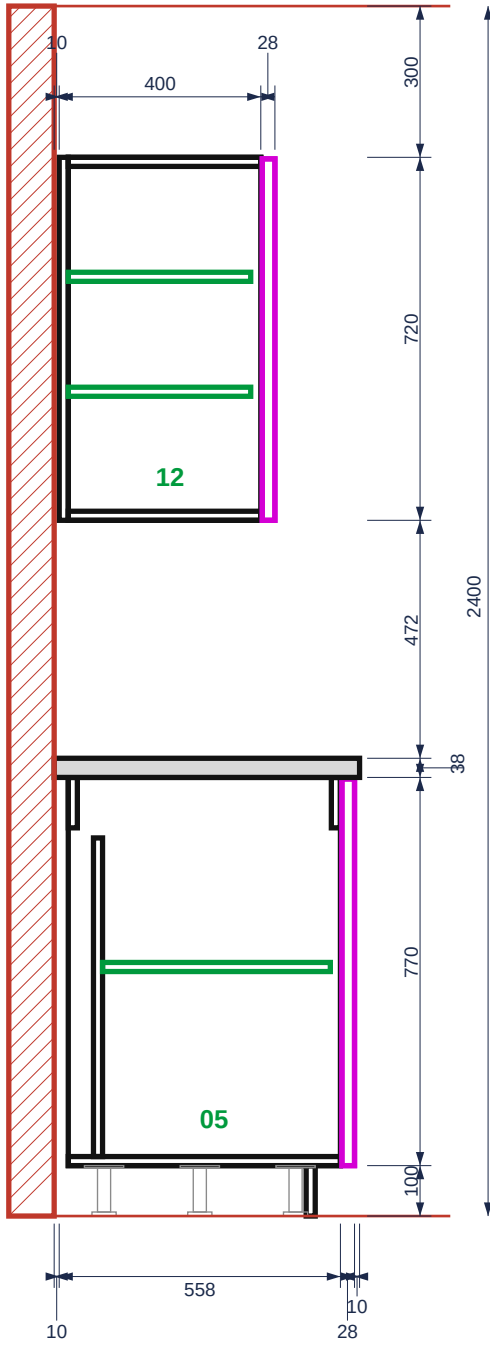

SECTION B-B · through units 05 and 12
looking along the wall, towards its start

KEY PLAN

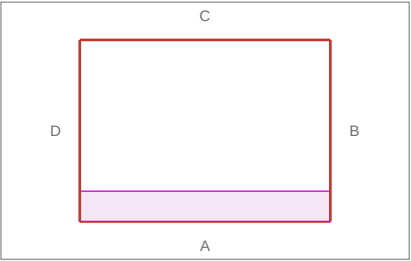

LEGEND

- Fronts (doors, drawer fronts)
- Carcass
- Hidden / above the cut
- Unit number
- Hardware, appliance space
- Building (walls, floor, ceiling)
- Dimensions in mm

NOTES

- All dimensions in millimetres. Do not scale off this drawing; work to figured dimensions.
- Carcass and fronts as the cut list, sheet with the materials.
- Appliances and worktop are shown for position only, supplied by others unless stated.
- Site dimensions to be checked before cutting.

STATUS

- A Preliminary
- B For approval
- C For production

Approved: Date:

LOGO
(Settings)

CABINET CORE
Bespoke fitted furniture
London
hello@cabinetcore.example

CLIENT

AP&W

SITE ADDRESS

3-7 Herbal Hill, 1st floor

PROPERTY OF

CABINET CORE. Not to be copied without consent.

PROJECT

3-7 Herbal Hill, 1st floor

DRAWING

05 · Wall A · Sections A-A and B-B

DRAWING No

032-2026-05

DRAWN

PT

CHECKED

DATE

08.02.2026

JOB No

032/2026

SCALE

1:15 @ A3

PAPER

A3

REV


A

SHEET


05 / 09

06 · WALL A · PERSPECTIVE VIEW

Line perspective from the room, eye height 1650. Not to scale; for orientation only.

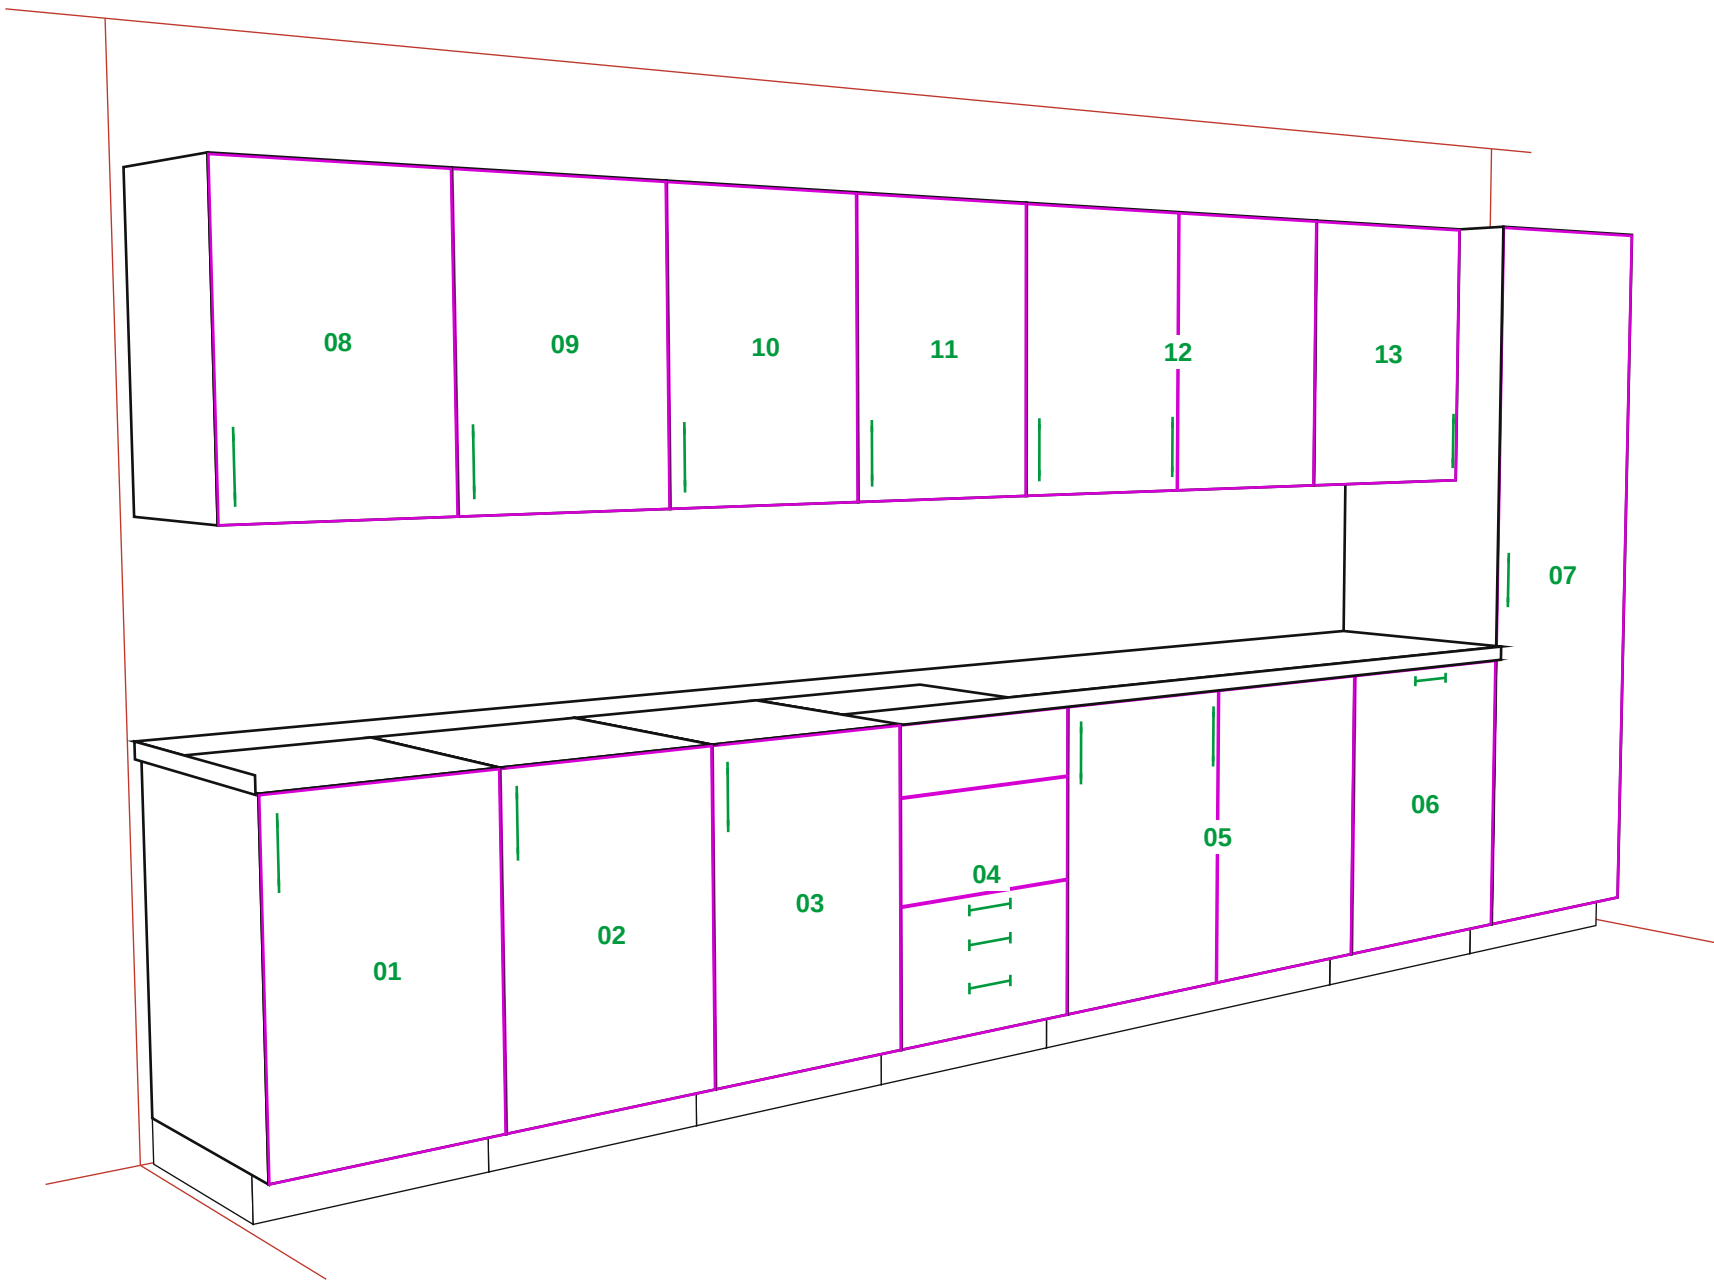

KEY PLAN

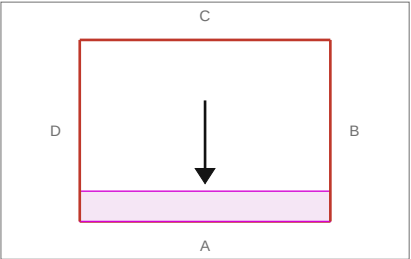

NOTES

1. Unit numbers as on the elevations.
2. Drawn from the same model as every other sheet; it cannot disagree with them.

STATUS

- ☐ A Preliminary
☒ B For approval
☐ C For production

Approved: _____ Date: _____

LOGO
(Settings)

CABINET CORE

Bespoke fitted furniture
London
hello@cabinetcore.example

CLIENT

AP&W

SITE ADDRESS

3-7 Herbal Hill, 1st floor

PROPERTY OF

CABINET CORE. Not to be copied without consent.

PROJECT

3-7 Herbal Hill, 1st floor

DRAWING

06 · Wall A · Perspective view

DRAWING No

032-2026-06

DRAWN

PT

CHECKED

DATE

08.02.2026

JOB No

032/2026

SCALE

NTS

PAPER

A3

REV


A

SHEET

06 / 09

07 · VISUALISATION

Rendered from the 3D scene with the fixed export lighting rig, the same rig on every sheet, so two decors compare.

 

FINISHES


FRONTS
not chosen yet

CARCASS
not chosen yet

WORKTOP
by others

Colours are screen approximations; confirm against physical samples.

KEY PLAN

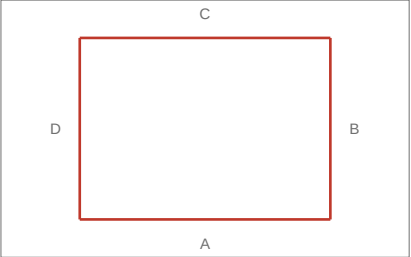

NOTES

1. Worktop, sink, taps and appliances are indicative, supplied by others.

STATUS

- ☐ A Preliminary
- ☒ B For approval
- ☐ C For production

Approved: Date:

LOGO
(Settings)

CABINET CORE

Bespoke fitted furniture
London
hello@cabinetcore.example

CLIENT

AP&W

SITE ADDRESS

3-7 Herbal Hill, 1st floor

PROPERTY OF

CABINET CORE. Not to be copied without consent.

PROJECT

3-7 Herbal Hill, 1st floor

DRAWING

07 · Visualisation

DRAWING No

032-2026-07

DRAWN

PT

CHECKED

DATE

08.02.2026

JOB No

032/2026

SCALE

NTS

PAPER

A3

REV

A

SHEET

07 / 09

08 · CUT LIST AND MATERIALS

Every panel per unit from the engine, the same numbers the CNC sheets and the BOM carry. Fronts in magenta.

UNIT 01 BUD 520 <table><tr><td>BUL</td><td>1 x</td><td>540 x 770</td><td>t18</td></tr><tr><td>BUR</td><td>1 x</td><td>540 x 770</td><td>t18</td></tr><tr><td>TOP</td><td>1 x</td><td>484 x 540</td><td>t18</td></tr><tr><td>BOTTOM</td><td>1 x</td><td>484 x 540</td><td>t18</td></tr><tr><td>BACK</td><td>1 x</td><td>520 x 770</td><td>t18</td></tr><tr><td>SHELF-1</td><td>1 x</td><td>480 x 520</td><td>t18</td></tr><tr><td>PLINTH</td><td>1 x</td><td>520 x 100</td><td>t18</td></tr><tr><td>01-F</td><td>1 x</td><td>517 x 767</td><td>t25</td></tr></table> 6 carcass panels · 2.00 m² · edging 2.99 m · fronts 0.45 m²	BUL	1 x	540 x 770	t18	BUR	1 x	540 x 770	t18	TOP	1 x	484 x 540	t18	BOTTOM	1 x	484 x 540	t18	BACK	1 x	520 x 770	t18	SHELF-1	1 x	480 x 520	t18	PLINTH	1 x	520 x 100	t18	01-F	1 x	517 x 767	t25	UNIT 04 BUDR 520 <table><tr><td>BUL</td><td>1 x</td><td>540 x 770</td><td>t18</td></tr><tr><td>BUR</td><td>1 x</td><td>540 x 770</td><td>t18</td></tr><tr><td>TOP</td><td>1 x</td><td>484 x 540</td><td>t18</td></tr><tr><td>BOTTOM</td><td>1 x</td><td>484 x 540</td><td>t18</td></tr><tr><td>BACK</td><td>1 x</td><td>520 x 770</td><td>t18</td></tr><tr><td>D1-SL</td><td>1 x</td><td>490 x 237</td><td>t18</td></tr><tr><td>D1-SR</td><td>1 x</td><td>490 x 237</td><td>t18</td></tr><tr><td>D2-SL</td><td>1 x</td><td>490 x 178</td><td>t18</td></tr><tr><td>D2-SR</td><td>1 x</td><td>490 x 178</td><td>t18</td></tr><tr><td>D3-SL</td><td>1 x</td><td>490 x 118</td><td>t18</td></tr><tr><td>D3-SR</td><td>1 x</td><td>490 x 118</td><td>t18</td></tr><tr><td>D1-BF</td><td>1 x</td><td>438 x 203</td><td>t18</td></tr><tr><td>D1-BB</td><td>1 x</td><td>438 x 203</td><td>t18</td></tr><tr><td>D2-BF</td><td>1 x</td><td>438 x 144</td><td>t18</td></tr><tr><td>D2-BB</td><td>1 x</td><td>438 x 144</td><td>t18</td></tr><tr><td>D3-BF</td><td>1 x</td><td>438 x 84</td><td>t18</td></tr><tr><td>D3-BB</td><td>1 x</td><td>438 x 84</td><td>t18</td></tr><tr><td>D1-DNO</td><td>1 x</td><td>451 x 490</td><td>t18</td></tr><tr><td>D2-DNO</td><td>1 x</td><td>451 x 490</td><td>t18</td></tr><tr><td>D3-DNO</td><td>1 x</td><td>451 x 490</td><td>t18</td></tr><tr><td>04-F1</td><td>1 x</td><td>517 x 338</td><td>t25</td></tr><tr><td>04-F2</td><td>1 x</td><td>517 x 254</td><td>t25</td></tr><tr><td>04-F3</td><td>1 x</td><td>517 x 169</td><td>t25</td></tr><tr><td>PLINTH</td><td>1 x</td><td>520 x 100</td><td>t18</td></tr></table> 20 carcass panels · 3.32 m² · edging 2.51 m · fronts 0.45 m²	BUL	1 x	540 x 770	t18	BUR	1 x	540 x 770	t18	TOP	1 x	484 x 540	t18	BOTTOM	1 x	484 x 540	t18	BACK	1 x	520 x 770	t18	D1-SL	1 x	490 x 237	t18	D1-SR	1 x	490 x 237	t18	D2-SL	1 x	490 x 178	t18	D2-SR	1 x	490 x 178	t18	D3-SL	1 x	490 x 118	t18	D3-SR	1 x	490 x 118	t18	D1-BF	1 x	438 x 203	t18	D1-BB	1 x	438 x 203	t18	D2-BF	1 x	438 x 144	t18	D2-BB	1 x	438 x 144	t18	D3-BF	1 x	438 x 84	t18	D3-BB	1 x	438 x 84	t18	D1-DNO	1 x	451 x 490	t18	D2-DNO	1 x	451 x 490	t18	D3-DNO	1 x	451 x 490	t18	04-F1	1 x	517 x 338	t25	04-F2	1 x	517 x 254	t25	04-F3	1 x	517 x 169	t25	PLINTH	1 x	520 x 100	t18	UNIT 07 FRIDGE 600 <table><tr><td>BUL</td><td>1 x</td><td>540 x 2000</td><td>t18</td></tr><tr><td>BUR</td><td>1 x</td><td>540 x 2000</td><td>t18</td></tr><tr><td>TOP</td><td>1 x</td><td>564 x 540</td><td>t18</td></tr><tr><td>BOTTOM</td><td>1 x</td><td>564 x 540</td><td>t18</td></tr><tr><td>FIXED</td><td>1 x</td><td>564 x 540</td><td>t18</td></tr><tr><td>RAIL1</td><td>1 x</td><td>600 x 200</td><td>t18</td></tr><tr><td>RAIL2</td><td>1 x</td><td>600 x 200</td><td>t18</td></tr><tr><td>BACK</td><td>1 x</td><td>600 x 196</td><td>t18</td></tr><tr><td>SPURS</td><td>1 x</td><td>556 x 160</td><td>t18</td></tr><tr><td>PLINTH</td><td>1 x</td><td>600 x 100</td><td>t18</td></tr><tr><td>07-F</td><td>1 x</td><td>597 x 1997</td><td>t25</td></tr></table> 9 carcass panels · 3.52 m² · edging 5.69 m · fronts 1.25 m²	BUL	1 x	540 x 2000	t18	BUR	1 x	540 x 2000	t18	TOP	1 x	564 x 540	t18	BOTTOM	1 x	564 x 540	t18	FIXED	1 x	564 x 540	t18	RAIL1	1 x	600 x 200	t18	RAIL2	1 x	600 x 200	t18	BACK	1 x	600 x 196	t18	SPURS	1 x	556 x 160	t18	PLINTH	1 x	600 x 100	t18	07-F	1 x	597 x 1997	t25	UNIT 11 WUD 520 <table><tr><td>BUL</td><td>1 x</td><td>382 x 720</td><td>t18</td></tr><tr><td>BUR</td><td>1 x</td><td>382 x 720</td><td>t18</td></tr><tr><td>TOP</td><td>1 x</td><td>484 x 382</td><td>t18</td></tr><tr><td>BOTTOM</td><td>1 x</td><td>484 x 382</td><td>t18</td></tr><tr><td>BACK</td><td>1 x</td><td>520 x 720</td><td>t18</td></tr><tr><td>SHELF-1</td><td>1 x</td><td>480 x 362</td><td>t18</td></tr><tr><td>SHELF-2</td><td>1 x</td><td>480 x 362</td><td>t18</td></tr><tr><td>11-F</td><td>1 x</td><td>517 x 717</td><td>t25</td></tr></table> 7 carcass panels · 1.64 m² · edging 3.37 m · fronts 0.37 m²	BUL	1 x	382 x 720	t18	BUR	1 x	382 x 720	t18	TOP	1 x	484 x 382	t18	BOTTOM	1 x	484 x 382	t18	BACK	1 x	520 x 720	t18	SHELF-1	1 x	480 x 362	t18	SHELF-2	1 x	480 x 362	t18	11-F	1 x	517 x 717	t25
BUL	1 x	540 x 770	t18	
BUR	1 x	540 x 770	t18	
TOP	1 x	484 x 540	t18	
BOTTOM	1 x	484 x 540	t18	
BACK	1 x	520 x 770	t18	
SHELF-1	1 x	480 x 520	t18	
PLINTH	1 x	520 x 100	t18	
01-F	1 x	517 x 767	t25	
BUL	1 x	540 x 770	t18	
BUR	1 x	540 x 770	t18	
TOP	1 x	484 x 540	t18	
BOTTOM	1 x	484 x 540	t18	
BACK	1 x	520 x 770	t18	
D1-SL	1 x	490 x 237	t18	
D1-SR	1 x	490 x 237	t18	
D2-SL	1 x	490 x 178	t18	
D2-SR	1 x	490 x 178	t18	
D3-SL	1 x	490 x 118	t18	
D3-SR	1 x	490 x 118	t18	
D1-BF	1 x	438 x 203	t18	
D1-BB	1 x	438 x 203	t18	
D2-BF	1 x	438 x 144	t18	
D2-BB	1 x	438 x 144	t18	
D3-BF	1 x	438 x 84	t18	
D3-BB	1 x	438 x 84	t18	
D1-DNO	1 x	451 x 490	t18	
D2-DNO	1 x	451 x 490	t18	
D3-DNO	1 x	451 x 490	t18	
04-F1	1 x	517 x 338	t25	
04-F2	1 x	517 x 254	t25	
04-F3	1 x	517 x 169	t25	
PLINTH	1 x	520 x 100	t18	
BUL	1 x	540 x 2000	t18	
BUR	1 x	540 x 2000	t18	
TOP	1 x	564 x 540	t18	
BOTTOM	1 x	564 x 540	t18	
FIXED	1 x	564 x 540	t18	
RAIL1	1 x	600 x 200	t18	
RAIL2	1 x	600 x 200	t18	
BACK	1 x	600 x 196	t18	
SPURS	1 x	556 x 160	t18	
PLINTH	1 x	600 x 100	t18	
07-F	1 x	597 x 1997	t25	
BUL	1 x	382 x 720	t18	
BUR	1 x	382 x 720	t18	
TOP	1 x	484 x 382	t18	
BOTTOM	1 x	484 x 382	t18	
BACK	1 x	520 x 720	t18	
SHELF-1	1 x	480 x 362	t18	
SHELF-2	1 x	480 x 362	t18	
11-F	1 x	517 x 717	t25	
UNIT 02 BUD 520 <table><tr><td>BUL</td><td>1 x</td><td>540 x 770</td><td>t18</td></tr><tr><td>BUR</td><td>1 x</td><td>540 x 770</td><td>t18</td></tr><tr><td>TOP</td><td>1 x</td><td>484 x 540</td><td>t18</td></tr><tr><td>BOTTOM</td><td>1 x</td><td>484 x 540</td><td>t18</td></tr><tr><td>BACK</td><td>1 x</td><td>520 x 770</td><td>t18</td></tr><tr><td>SHELF-1</td><td>1 x</td><td>480 x 520</td><td>t18</td></tr><tr><td>PLINTH</td><td>1 x</td><td>520 x 100</td><td>t18</td></tr><tr><td>02-F</td><td>1 x</td><td>517 x 767</td><td>t25</td></tr></table> 6 carcass panels · 2.00 m² · edging 2.99 m · fronts 0.45 m²	BUL	1 x	540 x 770	t18	BUR	1 x	540 x 770	t18	TOP	1 x	484 x 540	t18	BOTTOM	1 x	484 x 540	t18	BACK	1 x	520 x 770	t18	SHELF-1	1 x	480 x 520	t18	PLINTH	1 x	520 x 100	t18	02-F	1 x	517 x 767	t25	UNIT 05 SINK 1040 <table><tr><td>BUL</td><td>1 x</td><td>540 x 770</td><td>t18</td></tr><tr><td>BUR</td><td>1 x</td><td>540 x 770</td><td>t18</td></tr><tr><td>BOTTOM</td><td>1 x</td><td>1004 x 540</td><td>t18</td></tr><tr><td>BACK</td><td>1 x</td><td>1000 x 632</td><td>t18</td></tr><tr><td>HOLDER-F</td><td>1 x</td><td>100 x 1004</td><td>t18</td></tr><tr><td>HOLDER-B</td><td>1 x</td><td>100 x 1004</td><td>t18</td></tr><tr><td>SHELF-1</td><td>1 x</td><td>1000 x 452</td><td>t18</td></tr><tr><td>PLINTH</td><td>1 x</td><td>1040 x 100</td><td>t18</td></tr><tr><td>05-FL</td><td>1 x</td><td>517 x 767</td><td>t25</td></tr><tr><td>05-FR</td><td>1 x</td><td>517 x 767</td><td>t25</td></tr></table> 7 carcass panels · 2.66 m² · edging 3.54 m · fronts 0.90 m²	BUL	1 x	540 x 770	t18	BUR	1 x	540 x 770	t18	BOTTOM	1 x	1004 x 540	t18	BACK	1 x	1000 x 632	t18	HOLDER-F	1 x	100 x 1004	t18	HOLDER-B	1 x	100 x 1004	t18	SHELF-1	1 x	1000 x 452	t18	PLINTH	1 x	1040 x 100	t18	05-FL	1 x	517 x 767	t25	05-FR	1 x	517 x 767	t25	UNIT 09 WUD 520 <table><tr><td>BUL</td><td>1 x</td><td>382 x 720</td><td>t18</td></tr><tr><td>BUR</td><td>1 x</td><td>382 x 720</td><td>t18</td></tr><tr><td>TOP</td><td>1 x</td><td>484 x 382</td><td>t18</td></tr><tr><td>BOTTOM</td><td>1 x</td><td>484 x 382</td><td>t18</td></tr><tr><td>BACK</td><td>1 x</td><td>520 x 720</td><td>t18</td></tr><tr><td>SHELF-1</td><td>1 x</td><td>480 x 362</td><td>t18</td></tr><tr><td>SHELF-2</td><td>1 x</td><td>480 x 362</td><td>t18</td></tr><tr><td>09-F</td><td>1 x</td><td>517 x 717</td><td>t25</td></tr></table> 7 carcass panels · 1.64 m² · edging 3.37 m · fronts 0.37 m²	BUL	1 x	382 x 720	t18	BUR	1 x	382 x 720	t18	TOP	1 x	484 x 382	t18	BOTTOM	1 x	484 x 382	t18	BACK	1 x	520 x 720	t18	SHELF-1	1 x	480 x 362	t18	SHELF-2	1 x	480 x 362	t18	09-F	1 x	517 x 717	t25	UNIT 12 WUD 1040 <table><tr><td>BUL</td><td>1 x</td><td>382 x 720</td><td>t18</td></tr><tr><td>BUR</td><td>1 x</td><td>382 x 720</td><td>t18</td></tr><tr><td>TOP</td><td>1 x</td><td>1004 x 382</td><td>t18</td></tr><tr><td>BOTTOM</td><td>1 x</td><td>1004 x 382</td><td>t18</td></tr><tr><td>BACK</td><td>1 x</td><td>1040 x 720</td><td>t18</td></tr><tr><td>SHELF-1</td><td>1 x</td><td>1000 x 362</td><td>t18</td></tr><tr><td>SHELF-2</td><td>1 x</td><td>1000 x 362</td><td>t18</td></tr><tr><td>12-FL</td><td>1 x</td><td>517 x 717</td><td>t25</td></tr><tr><td>12-FR</td><td>1 x</td><td>517 x 717</td><td>t25</td></tr></table> 7 carcass panels · 2.79 m² · edging 5.45 m · fronts 0.74 m²	BUL	1 x	382 x 720	t18	BUR	1 x	382 x 720	t18	TOP	1 x	1004 x 382	t18	BOTTOM	1 x	1004 x 382	t18	BACK	1 x	1040 x 720	t18	SHELF-1	1 x	1000 x 362	t18	SHELF-2	1 x	1000 x 362	t18	12-FL	1 x	517 x 717	t25	12-FR	1 x	517 x 717	t25	
BUL	1 x	540 x 770	t18	
BUR	1 x	540 x 770	t18	
TOP	1 x	484 x 540	t18	
BOTTOM	1 x	484 x 540	t18	
BACK	1 x	520 x 770	t18	
SHELF-1	1 x	480 x 520	t18	
PLINTH	1 x	520 x 100	t18	
02-F	1 x	517 x 767	t25	
BUL	1 x	540 x 770	t18	
BUR	1 x	540 x 770	t18	
BOTTOM	1 x	1004 x 540	t18	
BACK	1 x	1000 x 632	t18	
HOLDER-F	1 x	100 x 1004	t18	
HOLDER-B	1 x	100 x 1004	t18	
SHELF-1	1 x	1000 x 452	t18	
PLINTH	1 x	1040 x 100	t18	
05-FL	1 x	517 x 767	t25	
05-FR	1 x	517 x 767	t25	
BUL	1 x	382 x 720	t18	
BUR	1 x	382 x 720	t18	
TOP	1 x	484 x 382	t18	
BOTTOM	1 x	484 x 382	t18	
BACK	1 x	520 x 720	t18	
SHELF-1	1 x	480 x 362	t18	
SHELF-2	1 x	480 x 362	t18	
09-F	1 x	517 x 717	t25	
BUL	1 x	382 x 720	t18	
BUR	1 x	382 x 720	t18	
TOP	1 x	1004 x 382	t18	
BOTTOM	1 x	1004 x 382	t18	
BACK	1 x	1040 x 720	t18	
SHELF-1	1 x	1000 x 362	t18	
SHELF-2	1 x	1000 x 362	t18	
12-FL	1 x	517 x 717	t25	
12-FR	1 x	517 x 717	t25	
UNIT 03 BUD 520 <table><tr><td>BUL</td><td>1 x</td><td>540 x 770</td><td>t18</td></tr><tr><td>BUR</td><td>1 x</td><td>540 x 770</td><td>t18</td></tr><tr><td>TOP</td><td>1 x</td><td>484 x 540</td><td>t18</td></tr><tr><td>BOTTOM</td><td>1 x</td><td>484 x 540</td><td>t18</td></tr><tr><td>BACK</td><td>1 x</td><td>520 x 770</td><td>t18</td></tr><tr><td>SHELF-1</td><td>1 x</td><td>480 x 520</td><td>t18</td></tr><tr><td>PLINTH</td><td>1 x</td><td>520 x 100</td><td>t18</td></tr><tr><td>03-F</td><td>1 x</td><td>517 x 767</td><td>t25</td></tr></table> 6 carcass panels · 2.00 m² · edging 2.99 m · fronts 0.45 m²	BUL	1 x	540 x 770	t18	BUR	1 x	540 x 770	t18	TOP	1 x	484 x 540	t18	BOTTOM	1 x	484 x 540	t18	BACK	1 x	520 x 770	t18	SHELF-1	1 x	480 x 520	t18	PLINTH	1 x	520 x 100	t18	03-F	1 x	517 x 767	t25	UNIT 06 DW_PANEL 600 <table><tr><td>TOP</td><td>1 x</td><td>600 x 540</td><td>t18</td></tr><tr><td>PLINTH</td><td>1 x</td><td>600 x 100</td><td>t18</td></tr><tr><td>06-F</td><td>1 x</td><td>594 x 767</td><td>t25</td></tr></table> 1 carcass panel · 0.32 m² · edging 0.60 m · fronts 0.52 m²	TOP	1 x	600 x 540	t18	PLINTH	1 x	600 x 100	t18	06-F	1 x	594 x 767	t25	UNIT 10 WUD 520 <table><tr><td>BUL</td><td>1 x</td><td>382 x 720</td><td>t18</td></tr><tr><td>BUR</td><td>1 x</td><td>382 x 720</td><td>t18</td></tr><tr><td>TOP</td><td>1 x</td><td>484 x 382</td><td>t18</td></tr><tr><td>BOTTOM</td><td>1 x</td><td>484 x 382</td><td>t18</td></tr><tr><td>BACK</td><td>1 x</td><td>520 x 720</td><td>t18</td></tr><tr><td>SHELF-1</td><td>1 x</td><td>480 x 362</td><td>t18</td></tr><tr><td>SHELF-2</td><td>1 x</td><td>480 x 362</td><td>t18</td></tr><tr><td>10-F</td><td>1 x</td><td>517 x 717</td><td>t25</td></tr></table> 7 carcass panels · 1.64 m² · edging 3.37 m · fronts 0.37 m²	BUL	1 x	382 x 720	t18	BUR	1 x	382 x 720	t18	TOP	1 x	484 x 382	t18	BOTTOM	1 x	484 x 382	t18	BACK	1 x	520 x 720	t18	SHELF-1	1 x	480 x 362	t18	SHELF-2	1 x	480 x 362	t18	10-F	1 x	517 x 717	t25	UNIT 13 WUD 600 <table><tr><td>BUL</td><td>1 x</td><td>382 x 720</td><td>t18</td></tr><tr><td>BUR</td><td>1 x</td><td>382 x 720</td><td>t18</td></tr><tr><td>TOP</td><td>1 x</td><td>564 x 382</td><td>t18</td></tr><tr><td>BOTTOM</td><td>1 x</td><td>564 x 382</td><td>t18</td></tr><tr><td>BACK</td><td>1 x</td><td>600 x 720</td><td>t18</td></tr><tr><td>SHELF-1</td><td>1 x</td><td>560 x 362</td><td>t18</td></tr><tr><td>SHELF-2</td><td>1 x</td><td>560 x 362</td><td>t18</td></tr><tr><td>13-F</td><td>1 x</td><td>597 x 717</td><td>t25</td></tr></table> 7 carcass panels · 1.82 m² · edging 3.69 m · fronts 0.43 m²	BUL	1 x	382 x 720	t18	BUR	1 x	382 x 720	t18	TOP	1 x	564 x 382	t18	BOTTOM	1 x	564 x 382	t18	BACK	1 x	600 x 720	t18	SHELF-1	1 x	560 x 362	t18	SHELF-2	1 x	560 x 362	t18	13-F	1 x	597 x 717	t25	
BUL	1 x	540 x 770	t18	
BUR	1 x	540 x 770	t18	
TOP	1 x	484 x 540	t18	
BOTTOM	1 x	484 x 540	t18	
BACK	1 x	520 x 770	t18	
SHELF-1	1 x	480 x 520	t18	
PLINTH	1 x	520 x 100	t18	
03-F	1 x	517 x 767	t25	
TOP	1 x	600 x 540	t18	
PLINTH	1 x	600 x 100	t18	
06-F	1 x	594 x 767	t25	
BUL	1 x	382 x 720	t18	
BUR	1 x	382 x 720	t18	
TOP	1 x	484 x 382	t18	
BOTTOM	1 x	484 x 382	t18	
BACK	1 x	520 x 720	t18	
SHELF-1	1 x	480 x 362	t18	
SHELF-2	1 x	480 x 362	t18	
10-F	1 x	517 x 717	t25	
BUL	1 x	382 x 720	t18	
BUR	1 x	382 x 720	t18	
TOP	1 x	564 x 382	t18	
BOTTOM	1 x	564 x 382	t18	
BACK	1 x	600 x 720	t18	
SHELF-1	1 x	560 x 362	t18	
SHELF-2	1 x	560 x 362	t18	
13-F	1 x	597 x 717	t25	

TOTALS · 13 units

Carcass board	27.01 m²	Fronts	7.11 m²	Edging	95.4 m	Hinges	42	Legs	25	Runner pairs	3
---------------	----------	--------	---------	--------	--------	--------	----	------	----	--------------	---

STATUS

- ☐ A Preliminary
- ☒ B For approval
- ☐ C For production

Approved: Date:

LOGO
(Settings)

CABINET CORE

Bespoke fitted furniture

London
hello@cabinetcore.example

CLIENT

AP&W

SITE ADDRESS

3-7 Herbal Hill, 1st floor

PROPERTY OF

CABINET CORE. Not to be copied without consent.

PROJECT

3-7 Herbal Hill, 1st floor

DRAWING

08 · Cut list and materials

DRAWING No

032-2026-08

DRAWN

PT

CHECKED

DATE

08.02.2026

JOB No

032/2026

SCALE

n/a

PAPER

A3

REV

A

SHEET

08 / 09